Nr	Y	X	H	Kodi	Përshkrimi	Burimi
19	7507860.598	4699761.972	598.674	40	Shtëpi-Ndërtesë	PM
20	7507869.941	4699766.328	598.674	40	Shtëpi-Ndërtesë	PM
22	7507864.751	4699777.376	598.674	40	Shtëpi-Ndërtesë	PM
23	7507855.379	4699773.006	598.674	40	Shtëpi-Ndërtesë	PM

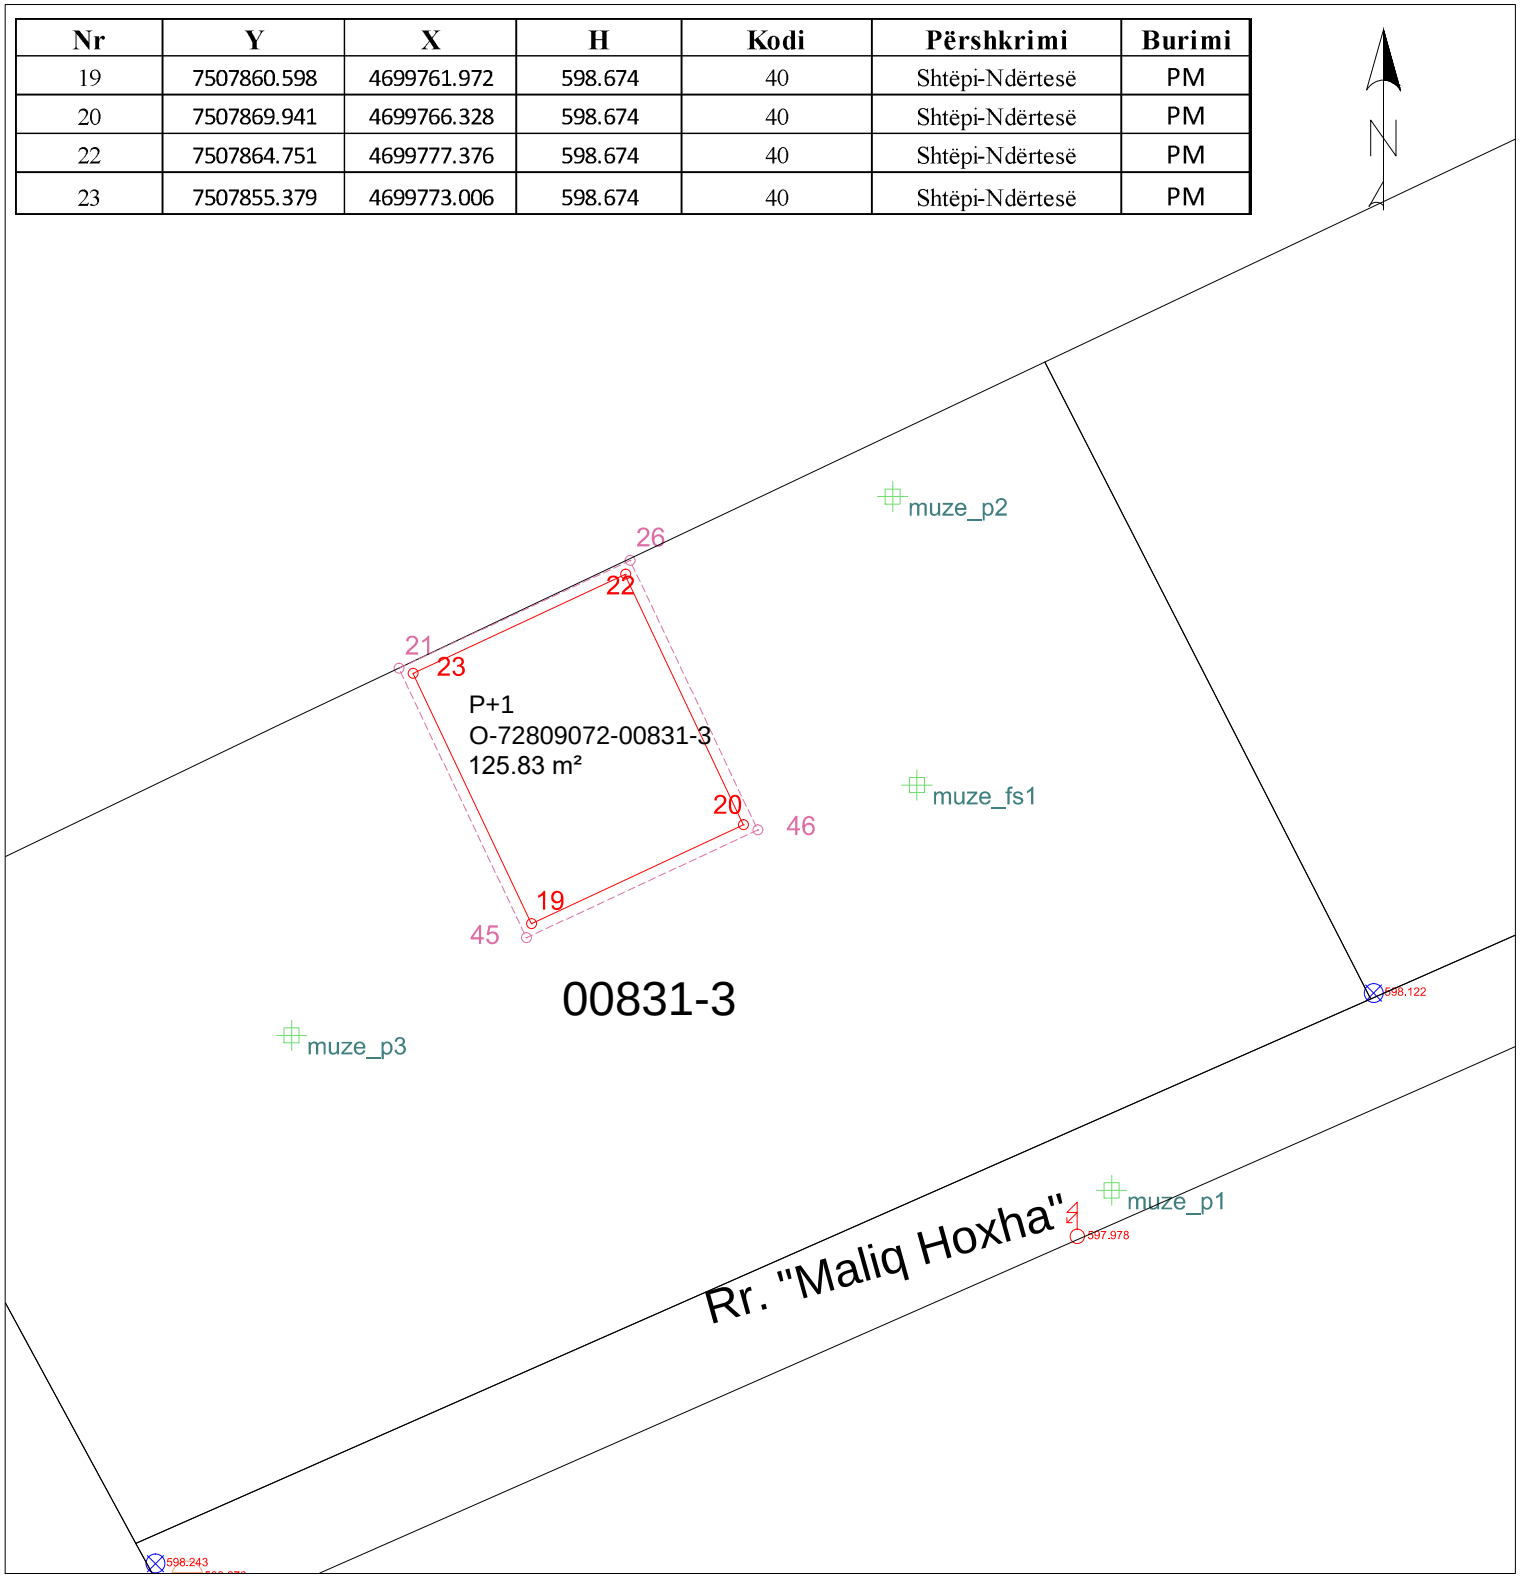

Republika e Kosovës

Qeveria -Vlada

Ministria e Mjedisit dhe Planifikimit Hapësinr /Ministarstv Sredine i Prstrng Planiranja

AGJENCIA KADASTRALE E KOSOVËS/ KATASTARSKA AGENCIJA KOSOVA

Situacioni i terrenit

Zyra kadastrale kmunale / pštinska katastarska kancelarija: Shtime

Zona kadastrale / Katastarska zona: Rashincë

Nr. i njësisë kadastrale / Br. katastarske jedinice : 00831-3

Numri i lëndës / Broj predmeta: _____

Shkalla e zvoglimit / Razmera plana 1: 250

Lista e koordinatave të pikave të matura:

Nr	Y	X	H	DSC
3	7507897.718	4699758.912	598.122	kyqjeuji
71	7507877.591	4699768.085	600.044	muze_fs1
73	7507886.171	4699750.216	598.151	muze_p1
74	7507876.521	4699780.801	598.504	muze_p2
75	7507850.027	4699757.049	598.555	muze_p3
19	7507860.598	4699761.972	598.674	perdhese
20	7507869.941	4699766.328	598.674	perdhese
22	7507864.751	4699777.376	598.674	perdhese
23	7507855.379	4699773.006	598.674	perdhese
2	7507905.420	4699760.042	598.120	pusetFeekkal
1	7507884.657	4699748.183	597.978	shtylElektrike
21	7507854.752	4699773.233	603.511	streha
26	7507864.947	4699777.986	603.511	streha
45	7507860.373	4699761.349	603.511	streha
46	7507870.568	4699766.102	603.511	streha

Shpjegues:

- Kufiri kadastral (nga SIKTK-G)
- Ndërtesa në trajtim për legalizim
- Ndërtesa tjera
- Aneks Ndërtimi
- Shtyllë elektrike
- Pusetë e ujësjellësit
- Pusetë e ujërave të zeza
- Strehët
- Kyqje në rrymë
- Pikë e objekteve fqinje
- Rr. Emri i rrugës
- Pikë e rrjetës gjeodezike
- Pikë e strehëve
- Pikë e terasës
- 10 Pikë e objektit
- Pikë e murit
- Pikë e kulmit

Rilevoi / Snimi: LIRIDON SEJDIU

(emri dhe mbiemri i gjedetit/kompanisë/ ime i prezime gedeta/ kompanije)

Nr. i licencës / Br. licence: 140

Data e rilevimit / Datum snimanja: 21.08.2025

Nënshkrimi / Potpis: _____

V.V.