Nr	Y	X	H	Kodi	Përshkrimi	Burimi
35	7507816.332	4699749.903	598.933	40	Shtëpi-Ndërtesë	PM
36	7507820.427	4699740.985	598.933	40	Shtëpi-Ndërtesë	PM
38	7507806.951	4699745.625	598.933	40	Shtëpi-Ndërtesë	PM
39	7507811.022	4699736.696	598.933	40	Shtëpi-Ndërtesë	PM

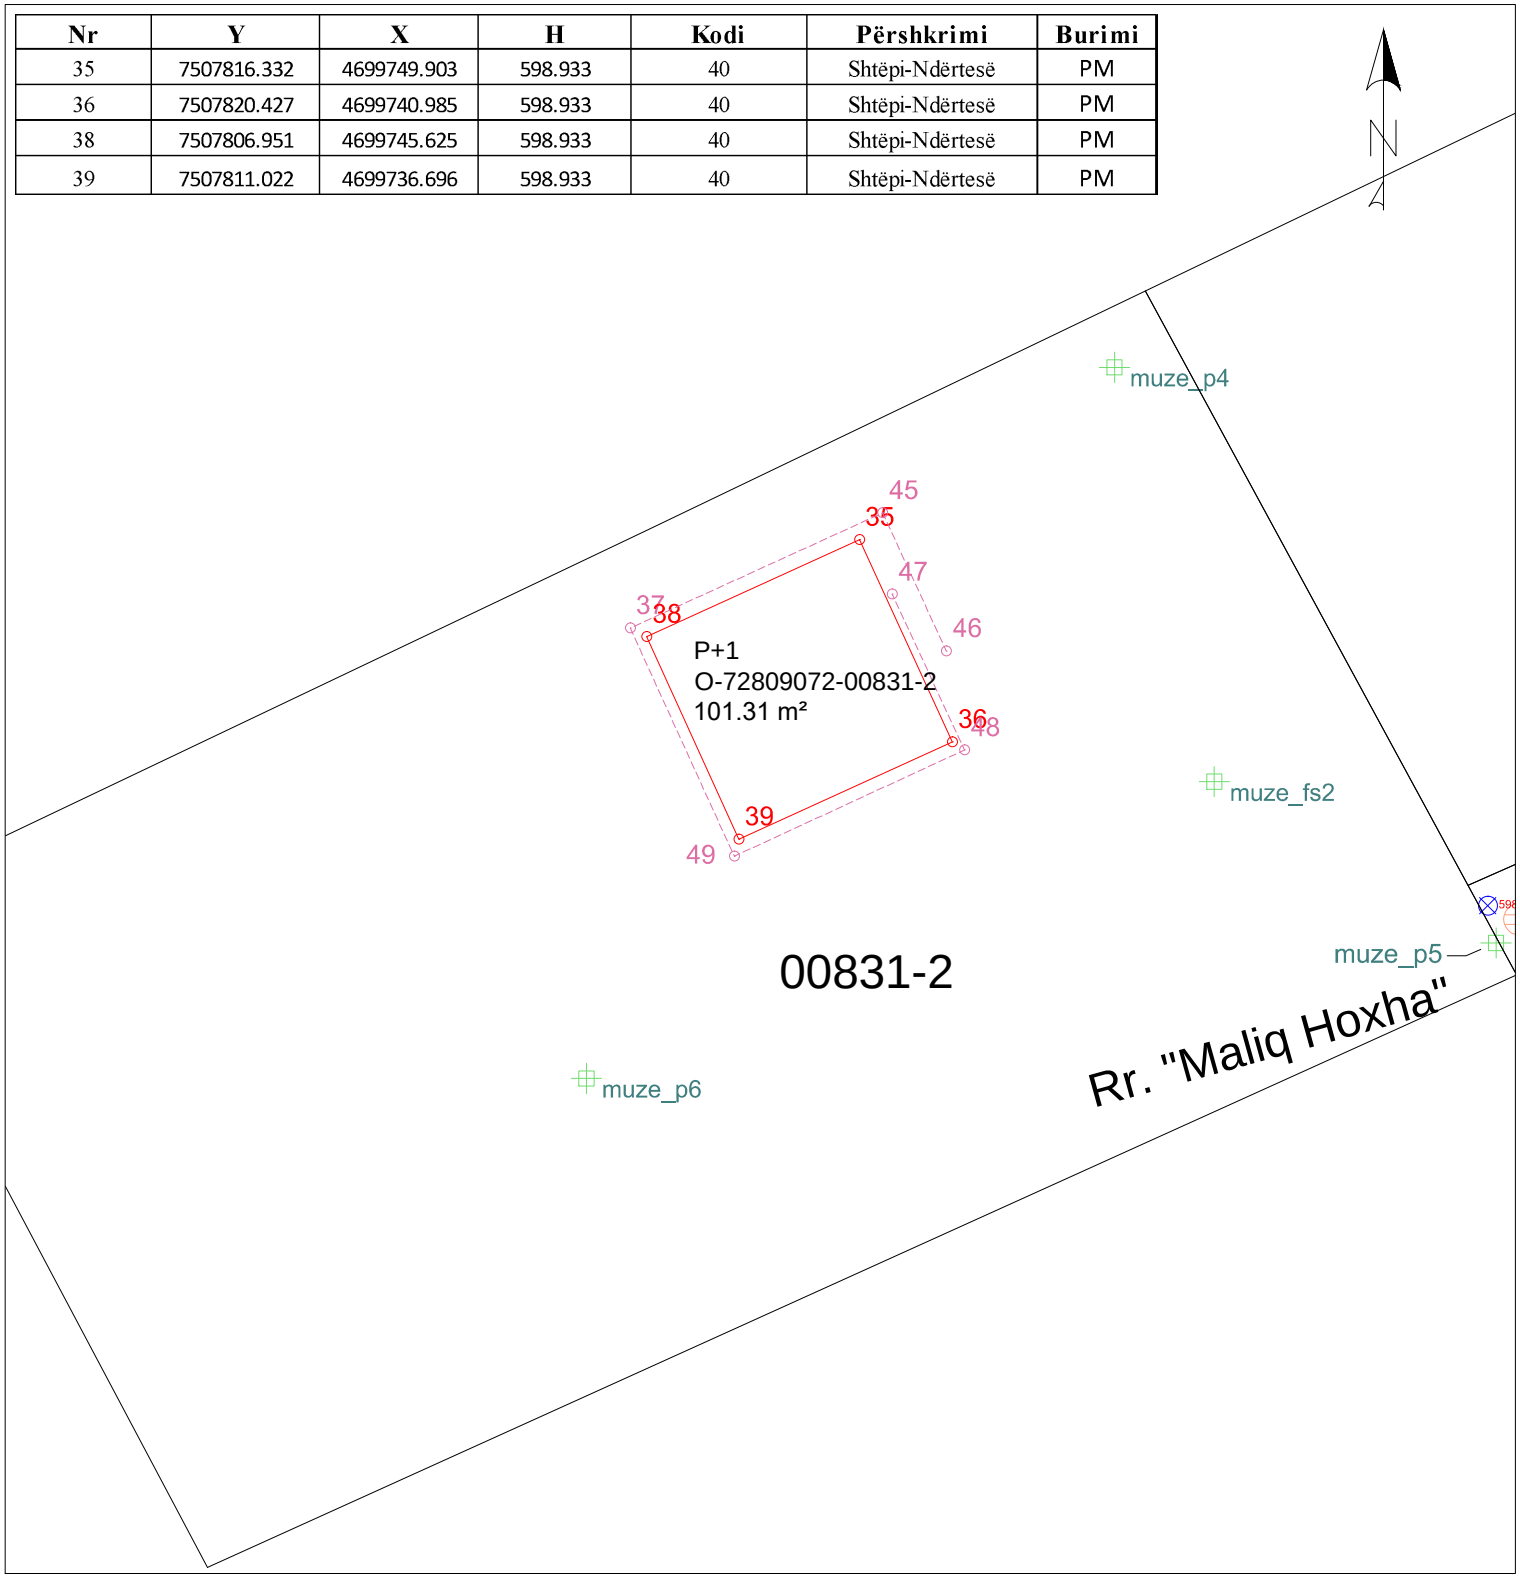

Republika e Kosovës

Qeveria -Vlada

Ministria e Mjedisit dhe Planifikimit Hapësinr /Ministarstv Sredine i Prstrng Planiranja

AGJENCIA KADASTRALE E KOSOVËS/ KATASTARSKA AGENCIJA KOSOVA

Situacioni i terrenit

Zyra kadastrale kmunale / pštinska katastarska kancelarija: Shtime

Zona kadastrale / Katastarska zona: Rashincë

Nr. i njësisë kadastrale / Br. katastarske jedinice : 00831-2

Numri i lëndës / Broj predmeta: _____

Shkalla e zvoglimit / Razmera plana 1: 250

Lista e koordinatave të pikave të matura:

Nr	Y	X	H	DSC
6	7507844.024	4699733.765	598.243	kyqje_uji
72	7507831.973	4699739.235	599.922	muze_fs2
76	7507827.573	4699757.498	598.724	muze_p4
77	7507844.391	4699732.123	598.320	muze_p5
78	7507804.298	4699726.152	598.541	muze_p6
35	7507816.332	4699749.903	598.933	perdhese
36	7507820.427	4699740.985	598.933	perdhese
38	7507806.951	4699745.625	598.933	perdhese
39	7507811.022	4699736.696	598.933	perdhese
5	7507845.426	4699733.174	598.278	pusetFeekkal
4	7507845.944	4699731.251	598.275	shtylElektrike
37	7507806.227	4699746.006	603.551	streha
45	7507817.356	4699751.081	603.500	streha
46	7507820.162	4699744.995	603.702	streha
47	7507817.776	4699747.500	605.993	streha
48	7507820.960	4699740.629	603.551	streha
49	7507810.814	4699735.947	603.551	streha

Shpjegues:

- Kufiri kadastral (nga SIKTK-G)
- Ndërtesa në trajtim për legalizim
- Ndërtesa tjera
- Aneks Ndërtimi
- Shtyllë elektrike
- Pusetë e ujësjellësit
- Pusetë e ujërave të zeza
- Strehët
- Kyqje në rrymë
- Pikë e objekteve fqinje
- Rr. Emri i rrugës
- Pikë e rrjetës gjeodezike
- Pikë e strehëve
- 81 Pikë e terasës
- 10 Pikë e objektit
- Pikë e murit
- Pikë e kulmit

Rilevoi / Snimi: LIRIDON SEJDIU

(emri dhe mbiemri i gjedetit/kompanisë/ ime i prezime gedeta/ kompanije)

Nr. i licencës / Br. licence: 140

Data e rilevimit / Datum snimanja: 21.08.2025

Nënshkrimi / Potpis: _____

V.V.