


Nr	Y	X	H	Kodi	Përshtkimi	Burimi
20	7507971.066	4699820.228	598.212	40	Shtëpi-Ndërtesë	PM
51	7507972.187	4699817.097	598.212	40	Shtëpi-Ndërtesë	PM
52	7507968.493	4699824.660	598.212	40	Shtëpi-Ndërtesë	PM
53	7507959.743	4699821.387	598.212	40	Shtëpi-Ndërtesë	PM
54	7507970.347	4699822.259	598.212	40	Shtëpi-Ndërtesë	PM
55	7507972.674	4699820.797	598.212	40	Shtëpi-Ndërtesë	PM
56	7507973.537	4699813.156	598.212	40	Shtëpi-Ndërtesë	PM
57	7507973.740	4699817.647	598.212	40	Shtëpi-Ndërtesë	PM
58	7507969.423	4699821.943	598.212	40	Shtëpi-Ndërtesë	PM
59	7507963.975	4699809.695	598.212	40	Shtëpi-Ndërtesë	PM



Republika e Kosovës
Qeveria - Vlada
Ministria e Mjedisit dhe Planifikimit Hapësinor /Ministarstv Sredine i Prstrg Planiranja
AGJENCIJA KADASTRALE E KOSOVËS / KATASTARSKA AGENCIJA KOSOVA

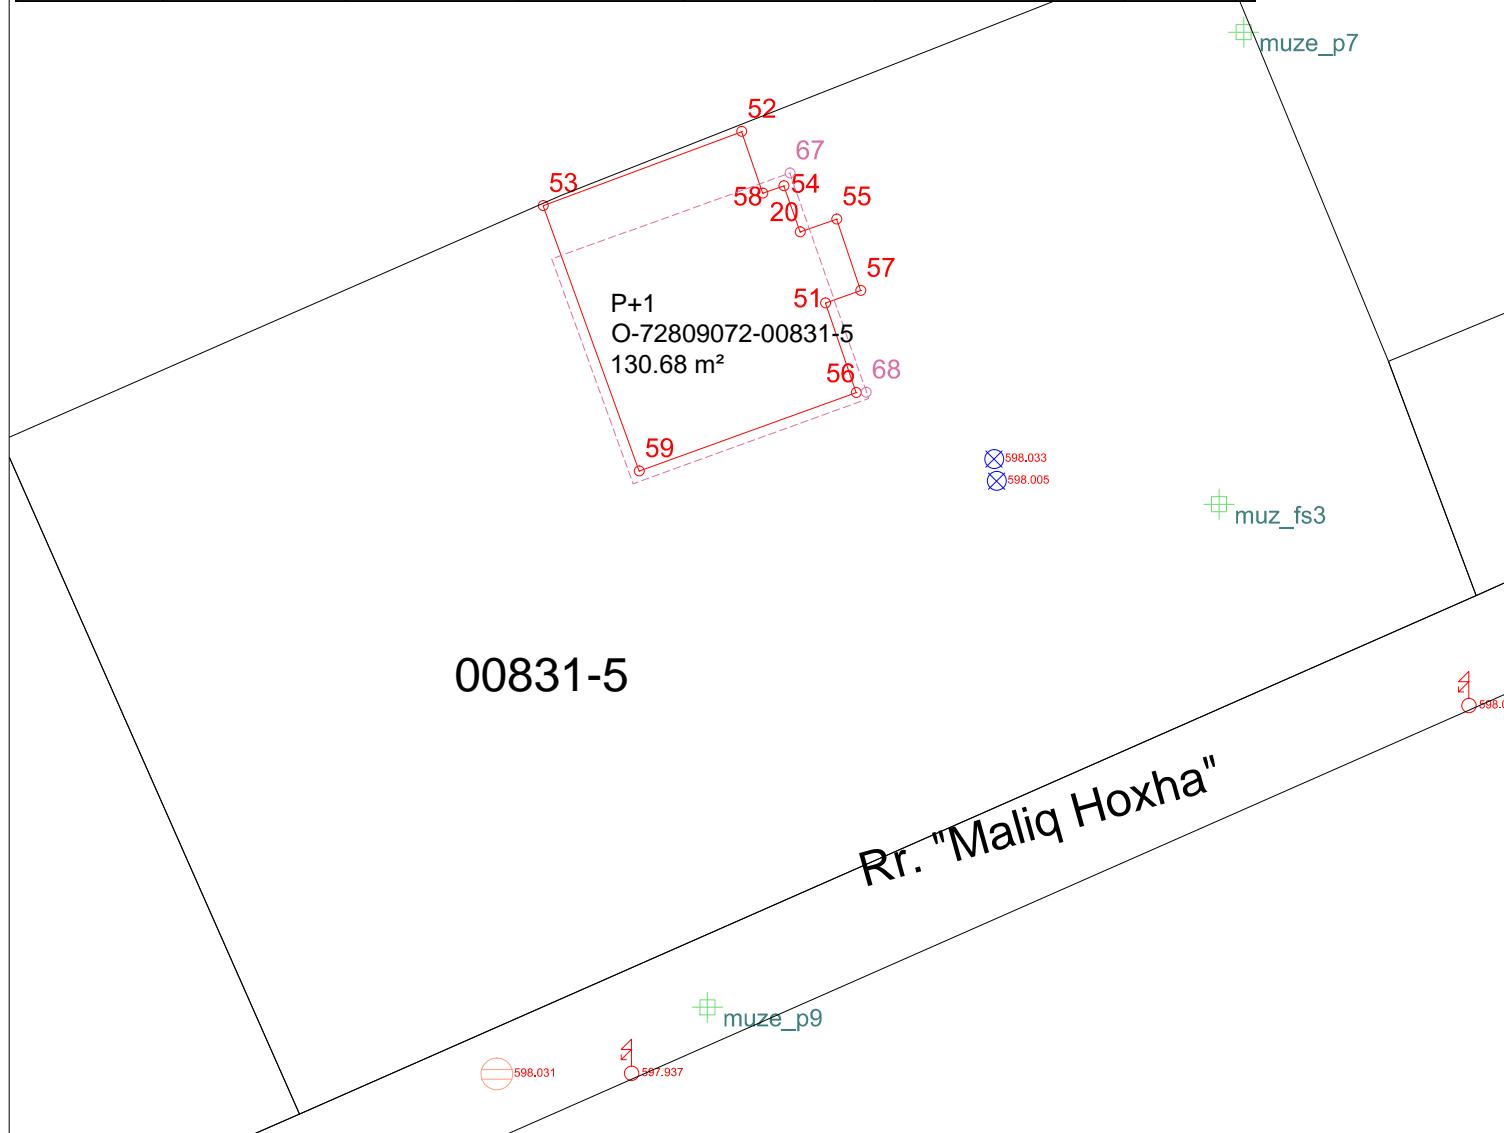

Situacioni i terrenit

Zyra kadastrale kmunale / pëtinska katastarska kancelarija: _____ Shtime

Zona kadastrale / Katastarska zona: _____ Rashincë

Nr. i njësisë kadastrale / Br. katastarske jedinice : _____ 00831-5

Numri i lëndës / Broj predmeta: _____

Shkalla e zgjegimit / Razmera plana 1: _____ 250

Lista e koordinatave të pikave të matura:

Nr	Y	X	H	DSC
17	7507979.618	4699810.221	598.033	kyqje_uji
18	7507979.732	4699809.254	598.005	kyqje_uji
70	7507989.536	4699808.230	599.720	muz_fs3
79	7507990.624	4699829.042	598.299	muze_p7
80	7508027.453	4699836.996	598.087	muze_p8
81	7507966.986	4699786.056	598.045	muze_p9
20	7507971.066	4699820.228	598.212	perdhese
51	7507972.187	4699817.097	598.212	perdhese
52	7507968.493	4699824.660	598.212	perdhese
53	7507959.743	4699821.387	598.212	perdhese
54	7507970.347	4699822.259	598.212	perdhese
55	7507972.674	4699820.797	598.212	perdhese
56	7507973.537	4699813.156	598.212	perdhese
57	7507973.740	4699817.647	598.212	perdhese
58	7507969.423	4699821.943	598.212	perdhese
59	7507963.975	4699809.695	598.212	perdhese
10	7508004.300	4699803.764	598.085	pusetFeekkal
9	7508000.545	4699799.346	598.059	shtylElektrike
15	7507998.199	4699834.710	598.376	shtylElektrike
67	7507970.616	4699822.825	601.412	streha
68	7507973.978	4699813.163	602.995	streha

Shpjegues:

Kufiri kadastral (nga SIKTK-G)

Rr.

Emri i rrugës

Ndërtesa në trajtim për legalizim

Pikë e rrejtës gjeodezike

Ndërtesa tjera

Pikë e strehëve

Aneks Ndërtimi

Pikë e terasës

Shtyllë elektrike

Pikë e objektit

Pusetë e ujësjellësit

Pikë e murit

Pusetë e ujërave të zeza

Pikë e kulmit

Strehët

Kyqje në rrymë

Rilevoi / Snimi: _____ LIRDON SEJDIU

(emri dhe mbiemri i gjedjetit/kompanisë/ ime i prezime gedeta/ kompanije)

Nr. i licencës / Br. licence: _____ 140

Data e rilevimit / Datum snimanja: _____ 21.08.2025

Nënshkrimi / Potpis: _____

V.V.

Nr	Y	X	H	Kodi	Përskrimi	Burimi
20	7507971.066	4699820.228	598.212	40	Shtëpi-Ndertesë	PM
51	7507972.187	4699817.097	598.212	40	Shtëpi-Ndertesë	PM
52	7507968.493	4699824.660	598.212	40	Shtëpi-Ndertesë	PM
53	7507959.743	4699821.387	598.212	40	Shtëpi-Ndertesë	PM
54	7507970.347	4699822.259	598.212	40	Shtëpi-Ndertesë	PM
55	7507972.674	4699820.797	598.212	40	Shtëpi-Ndertesë	PM
56	7507973.537	4699813.156	598.212	40	Shtëpi-Ndertesë	PM
57	7507973.740	4699817.647	598.212	40	Shtëpi-Ndertesë	PM
58	7507969.423	4699821.943	598.212	40	Shtëpi-Ndertesë	PM
59	7507963.975	4699809.695	598.212	40	Shtëpi-Ndertesë	PM



Republika e Kosovës
Qeveria - Vlada
Ministria e Mjedisit dhe Planifikimit Hapësinor /Ministarstv Sredine i Prstrg Planiranja
AGJENCIJA KADASTRALE E KOSOVËS / KATASTARSKA AGJENCIJA KOSOVA



Situacioni i terrenit

Orto 2004

Zyra kadastrale kmunale / pëtinska katastarska kancelarija: _____ Shtime

Zona kadastrale / Katastarska zona: _____ Rashincë

Nr. i njësisë kadastrale / Br. katastarske jedinice : _____ 00831-5

Numri i lëndës / Broj predmeta: _____

Shkalla e zgjegimit / Razmera plana 1: _____ 250

Lista e koordinatave të pikave të matura:

Nr	Y	X	H	DSC
17	7507979.618	4699810.221	598.033	kyqje_uji
18	7507979.732	4699809.254	598.005	kyqje_uji
70	7507989.536	4699808.230	599.720	muze_fs3
79	7507990.624	4699829.042	598.299	muze_p7
80	7508027.453	4699836.996	598.087	muze_p8
81	7507966.986	4699786.056	598.045	muze_p9
20	7507971.066	4699820.228	598.212	perdhese
51	7507972.187	4699817.097	598.212	perdhese
52	7507968.493	4699824.660	598.212	perdhese
53	7507959.743	4699821.387	598.212	perdhese
54	7507970.347	4699822.259	598.212	perdhese
55	7507972.674	4699820.797	598.212	perdhese
56	7507973.537	4699813.156	598.212	perdhese
57	7507973.740	4699817.647	598.212	perdhese
58	7507969.423	4699821.943	598.212	perdhese
59	7507963.975	4699809.695	598.212	perdhese
10	7508004.300	4699803.764	598.085	pusetFeekkal
9	7508000.545	4699799.346	598.059	shtylElektrike
15	7507998.199	4699834.710	598.376	shtylElektrike
67	7507970.616	4699822.825	601.412	streha
68	7507973.978	4699813.163	602.995	streha

Shpjegues:

- Kufiri kadastral (nga SIKTK-G)
- Ndërtesa në trajtim për legalizim
- Ndërtesa tjera
- Aneks Ndërtimi
- Shtylli elektrike
- Pusetë e ujësjellësit
- Pusetë e ujërave të zeza
- Strehët
- Kyqje në rrymë
- Rilevoi / Snimi: _____ LIRIDON SEJDIU
(emri dhe mbiemri i gjedjetit/kompanisë/ ime i prezime gedeta/ kompanije)
- Nr. i licencës / Br. licence: _____ 140
- Data e rilevimit / Datum snimanja: _____ 21.08.2025
- Nënshkrimi / Potpis: _____
V.V.

Nr	Y	X	H	Kodi	Përshtkimi	Burimi
20	7507971.066	4699820.228	598.212	40	Shtëpi-Ndërtesë	PM
51	7507972.187	4699817.097	598.212	40	Shtëpi-Ndërtesë	PM
52	7507968.493	4699824.660	598.212	40	Shtëpi-Ndërtesë	PM
53	7507959.743	4699821.387	598.212	40	Shtëpi-Ndërtesë	PM
54	7507970.347	4699822.259	598.212	40	Shtëpi-Ndërtesë	PM
55	7507972.674	4699820.797	598.212	40	Shtëpi-Ndërtesë	PM
56	7507973.537	4699813.156	598.212	40	Shtëpi-Ndërtesë	PM
57	7507973.740	4699817.647	598.212	40	Shtëpi-Ndërtesë	PM
58	7507969.423	4699821.943	598.212	40	Shtëpi-Ndërtesë	PM
59	7507963.975	4699809.695	598.212	40	Shtëpi-Ndërtesë	PM



Republika e Kosovës
Qeveria - Vlada
Ministria e Mjedisit dhe Planifikimit Hapësinor /Ministarstv Sredine i Prstrin Planiranja
AGJENCIJA KADASTRALE E KOSOVËS / KATASTARSKA AGENCJA KOSOVA



Situacioni i terrenit

Orto 2018

Zyra kadastrale kmunale / pëtinska katastarska kancelarija: _____ Shtime

Zona kadastrale / Katastarska zona: _____ Rashincë

Nr. i njësisë kadastrale / Br. katastarske jedinice : _____ 00831-5

Numri i lëndës / Broj predmeta: _____

Shkalla e zgjedhimit / Razmera plana 1: _____ 250

Lista e koordinatave të pikave të matura:

Nr	Y	X	H	DSC
17	7507979.618	4699810.221	598.033	kyqje_uji
18	7507979.732	4699809.254	598.005	kyqje_uji
70	7507989.536	4699808.230	599.720	muz_fs3
79	7507990.624	4699829.042	598.299	muze_p7
80	7508027.453	4699836.996	598.087	muze_p8
81	7507966.986	4699786.056	598.045	muze_p9
20	7507971.066	4699820.228	598.212	perdhese
51	7507972.187	4699817.097	598.212	perdhese
52	7507968.493	4699824.660	598.212	perdhese
53	7507959.743	4699821.387	598.212	perdhese
54	7507970.347	4699822.259	598.212	perdhese
55	7507972.674	4699820.797	598.212	perdhese
56	7507973.537	4699813.156	598.212	perdhese
57	7507973.740	4699817.647	598.212	perdhese
58	7507969.423	4699821.943	598.212	perdhese
59	7507963.975	4699809.695	598.212	perdhese
10	7508004.300	4699803.764	598.085	pusetFeekkal
9	7508000.545	4699799.346	598.059	shtylElektrike
15	7507998.199	4699834.710	598.376	shtylElektrike
67	7507970.616	4699822.825	601.412	streha
68	7507973.978	4699813.163	602.995	streha

Shpjegues:

Kufiri kadastral (nga SIKTK-G)

Ndërtesa në trajtim për legalizim

Ndërtesa tjera

Aneks Ndërtimi

Shtyllë elektrike

(○) Pusetë e ujësjellësit

(◐) Pusetë e ujërave të zeza

Strehët

(◐) Kyqje në rrymë

Rilevoi / Snimi: _____ LIRIDON SEJDIU

(emri dhe mbiemri i gjedjetit/kompanisë/ ime i prezime gedeta/ kompanije)

Nr. i licencës / Br. licence: _____ 140

Data e rilevimit / Datum snimanja: _____ 21.08.2025

Nënshkrimi / Potpis: _____

V.V.

Pikë e objekteve fqinje

Rr. Emri i rrugës

Pikë e rrjetës gjeodezike

Pikë e strehëve

Pikë e terasës

Pikë e objektit

Pikë e murit

Pikë e kulmit

10



Republika e Kosovës

Republika Kosova-Republic of Kosovo

Qeveria e Kosovës- Vlada Kosova- Government of Kosovo


Ministria e Infrastrukturës dhe Ambientit/ Ministrastvo Infrastrukture i Sredine/ Ministry of Infrastructure and Environment
AGJENCIA KADASTRALE E KOSOVËS/KOSOVSKA KATASTARSKA AGENCIJA/ KOSOVO CADASTRAL AGENCY

Komuna: Shtime
Numri i njësis kadastrale: 00831-5

Zona Kadastrale: Rashincë
Sistemi koordinat: KosovaRef01

Nr	Y	X	H	Kodi	Përshkrimi	Burimi
20	7507971.066	4699820.228	598.212	40	Shtëpi-Ndërtesë	PM
51	7507972.187	4699817.097	598.212	40	Shtëpi-Ndërtesë	PM
52	7507968.493	4699824.660	598.212	40	Shtëpi-Ndërtesë	PM
53	7507959.743	4699821.387	598.212	40	Shtëpi-Ndërtesë	PM
54	7507970.347	4699822.259	598.212	40	Shtëpi-Ndërtesë	PM
55	7507972.674	4699820.797	598.212	40	Shtëpi-Ndërtesë	PM
56	7507973.537	4699813.156	598.212	40	Shtëpi-Ndërtesë	PM
57	7507973.740	4699817.647	598.212	40	Shtëpi-Ndërtesë	PM
58	7507969.423	4699821.943	598.212	40	Shtëpi-Ndërtesë	PM
59	7507963.975	4699809.695	598.212	40	Shtëpi-Ndërtesë	PM

Gjeodeti / Kompania gjeodete e licencuar:	Liridon Sejdiu	Nënshkrimi dhe vula:	
Numri i licencës	140		

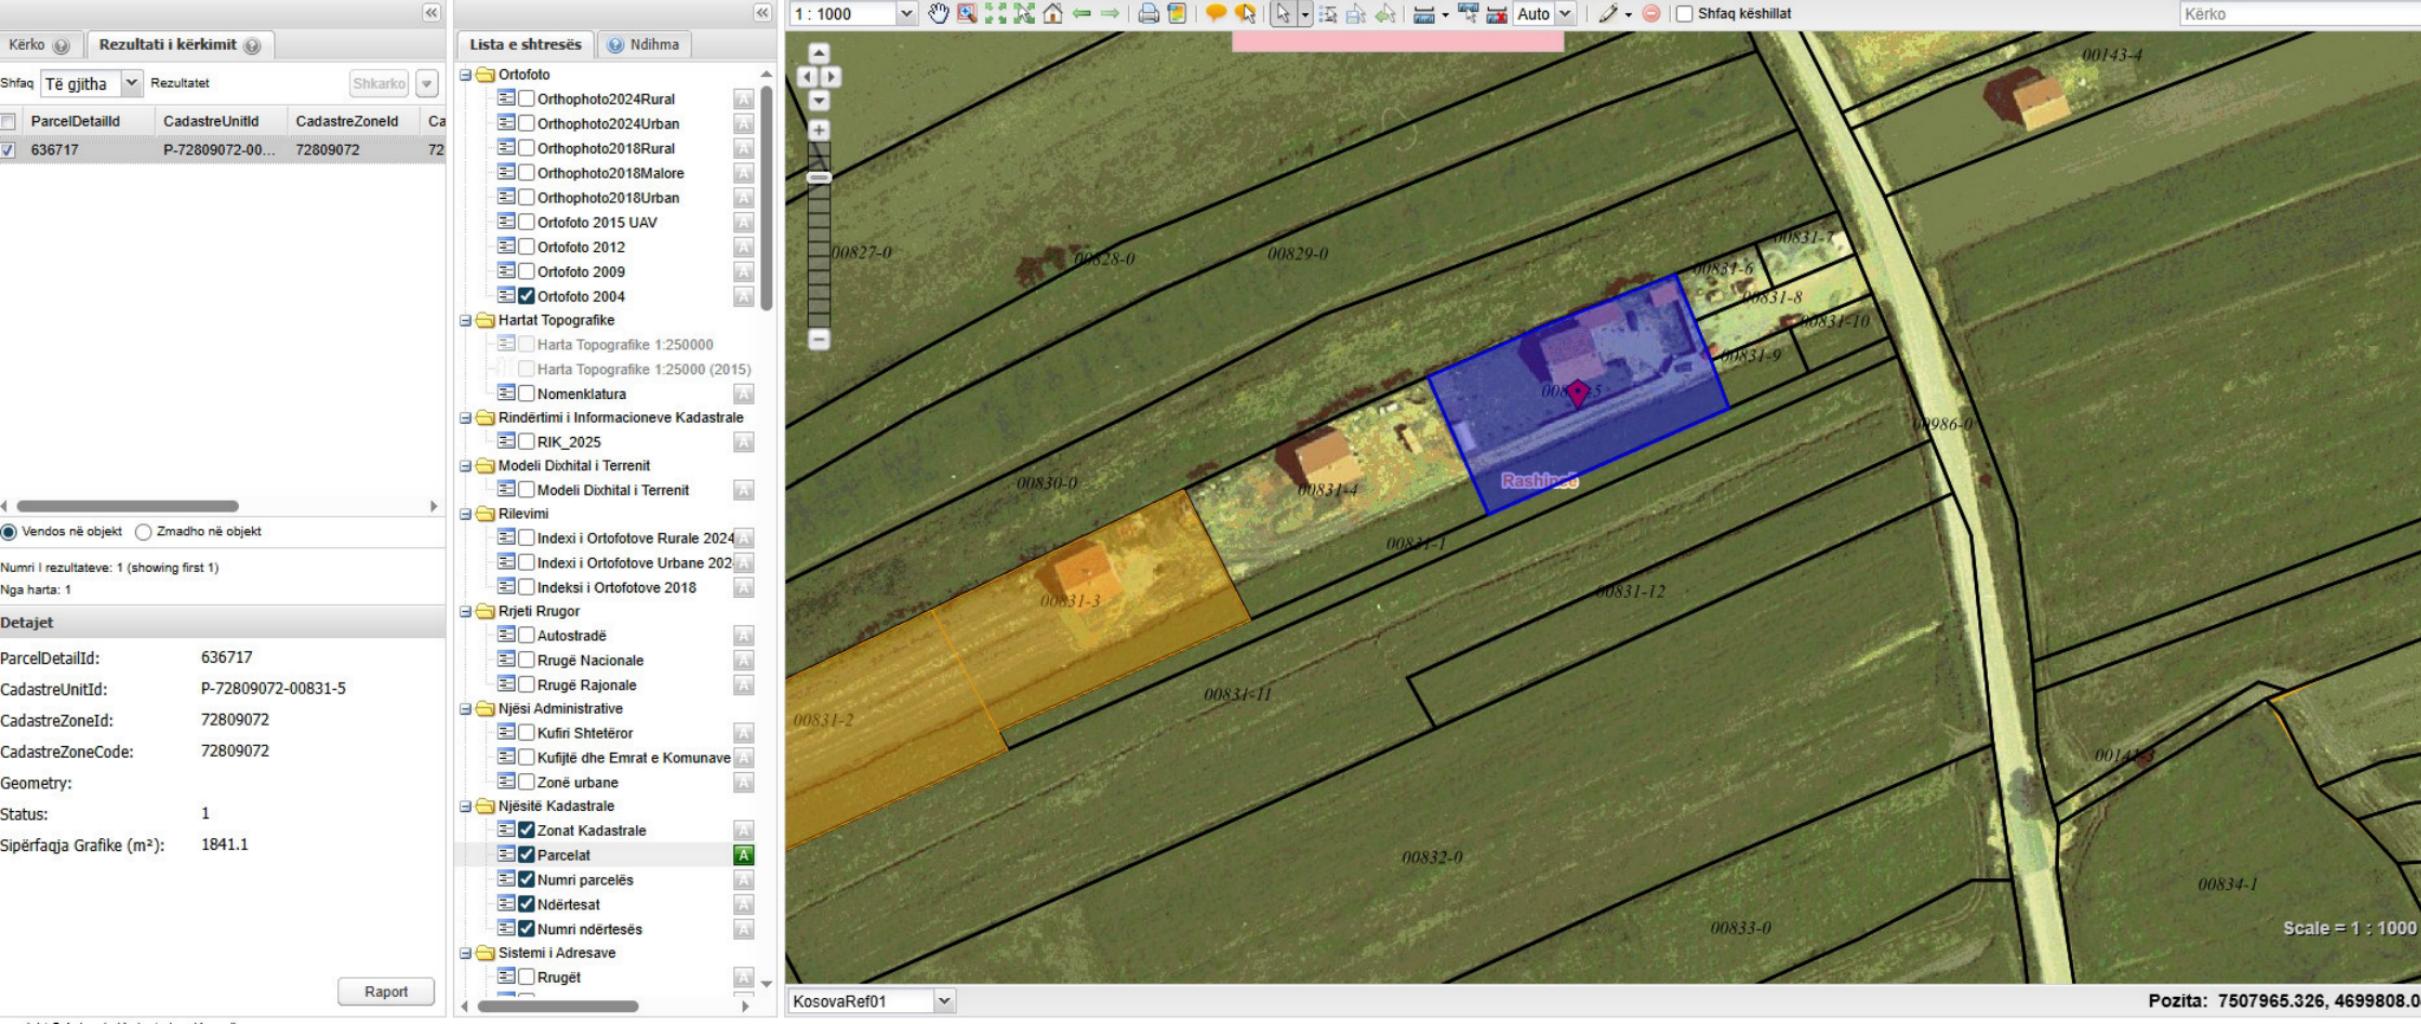

Kerko

Rezultati e kërkimit

Shfaq Të gjitha Rezultatet Shkarko

ParcelDetailId	CadastreUnitId	CadastreZoneId	Ca
636717	P-72809072-00...	72809072	72

Vendos në objekt Zmadho në objekt

Numi i rezultateve: 1 (showing first 1)
Nga harta: 1

Detajet

ParcelDetailId: 636717
CadastreUnitId: P-72809072-00831-5
CadastreZoneId: 72809072
CadastreZoneCode: 72809072
Geometry:
Status: 1
Sipërfaqja Grafike (m²): 1841.1

Rapor

Lista e shtresës Ndhima

- Ortofoto
 - Orthophoto2024Rural
 - Orthophoto2024Urban
 - Orthophoto2018Rural
 - Orthophoto2018Malore
 - Orthophoto2018Urban
 - Orthofoto 2015 UAV
 - Orthofoto 2012
 - Orthofoto 2009
 - Orthofoto 2004
- Hartat Topografike
 - Harta Topografike 1:250000
 - Harta Topografike 1:25000 (2015)
 - Nomenklatura
- Rindërtimi i Informacioneve Kadastrale
 - RIK_2025
- Modeli Dixhital i Terrenit
 - Modeli Dixhital i Terrenit
- Rilevimi
 - Indexi i Ortofotove Rurale 2024
 - Indexi i Ortofotove Urbane 2022
 - Indexi i Ortofotove 2018
- Rrjeti Rrugor
 - Autostradë
 - Rrugë Nacionale
 - Rrugë Rajonale
- Njësi Administrative
 - Kufiri Shtetëror
 - Kufijë dhe Emrat e Komunave
 - Zonë urbane
- Njësität Kadastrale
 - Zonat Kadastrale
 - Parcelat
 - Numri parcelës
 - Ndërfesat
 - Numri ndërtesës
- Sistemi i Adresave
 - Rrugët

1 : 1000

Auto Shfaq këshillat

00827-0 00828-0 00829-0 00830-0 00831-4 00831-5 00831-9 00831-10 00831-11 00831-12 00832-0 00833-0 00834-1 00143-4

Rashinca

KosovaRef01

Pozita: 7507964.766, 4699811.964

Scale = 1 : 1000

Zyra kadastrale komunale / Opštinska katastarska kancelarija: ShtimeNr. i njësisë kadastrale / Br. katastarske jedinice : 00831-5Zona kadastrale / Katastarska zona: Rashincë


Numri i lëndës / Broj predmeta: _____

Lloji i njësisë kadastrale / Vrsta katastarske jedinice : ShtëpiShkalla e zvoglimit / Razmera plana 1: 250**Republika e Kosovës****Republika Kosova-Republic of Kosovo****Qeveria -Vlada-Government****Ministria e Mjedisit dhe Planifikimit Hapësinor /Ministarstvo Sredine i Prostornog Planiranja/Ministry of Environment and Spatial Planning**

AGJENCIA KADASTRALE E KOSOVËS/KATASTARSKA AGECIJA KOSOVA/KOSOVA CADASTRAL AGENCY



Nr.	Y	X	H	D	Etazhi	Sqarim	Sipërfaqja (m ²)
20	7507971.07	4699820.23	598.21	perdhese			
51	7507972.19	4699817.10	598.21	perdhese			
52	7507968.49	4699824.66	598.21	perdhese			
53	7507959.74	4699821.39	598.21	perdhese			
54	7507970.35	4699822.26	598.21	perdhese			
55	7507972.67	4699820.80	598.21	perdhese			
56	7507973.54	4699813.16	598.21	perdhese			
57	7507973.74	4699817.65	598.21	perdhese			
58	7507969.42	4699821.94	598.21	perdhese			
59	7507963.98	4699809.70	598.21	perdhese			
Përdhesa						Përdhesa	130.68
Gjithsej:						Gjithsej:	130.68

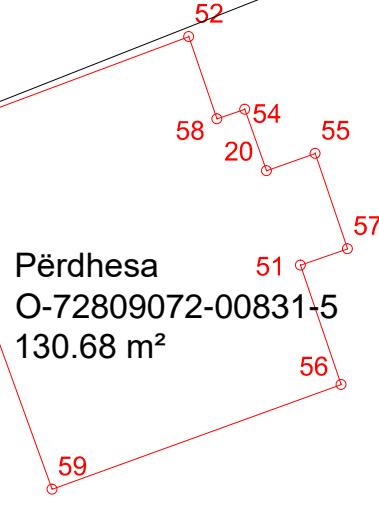**00831-5****Rr. "Maliq Hoxha"****LIRIDON SEJDIU**

(emri dhe mbiemri i gjyqetit/kompanisë/ ime i prezime geodeta/ kompanije)

Nr. i licencës / Br. licence: 140

V.V.

Aprovoi / Usvojio: _____

(emri dhe mbiemri i pësonit zyrtar/ ime i prezime sluzbeneg lica)

Nënshkrimi / Potpis: _____

Nënshkrimi / Potpis: _____

Data e rilevimit / Datum snimanja: 21.08.2025

Data e rilevimit / Datum snimanja: _____

Zyra kadastrale komunale / Opštinska katastarska kancelarija: ShtimeNr. i njësisë kadastrale / Br. katastarske jedinice : 00831-5Zona kadastrale / Katastarska zona: Rashincë


Numri i lëndës / Broj predmeta: _____

Lloji i njësisë kadastrale / Vrsta katastarske jedinice : ShtëpiShkalla e zvoglimit / Razmera plana 1: 250**Republika e Kosovës****Republika Kosova-Republic of Kosovo****Qeveria -Vlada-Government****Ministria e Mjedisit dhe Planifikimit Hapësinor /Ministarstvo Sredine i Prostornog Planiranja/Ministry of Environment and Spatial Planning**

AGJENCIA KADASTRALE E KOSOVËS/KATASTARSKA AGENCIJA KOSOVA/KOSOVA CADASTRAL AGENCY



Nr.	Y	X	H	D	Etazhi	Sqarim	Sipërfaqja (m ²)
24	7507960.69	4699818.78	600.54	katil	Kati 1	Kati 1	98.65
60	7507963.98	4699809.70	600.54	katil			
61	7507973.53	4699813.15	600.54	katil			
62	7507970.35	4699822.25	600.54	katil			
63	7507972.67	4699820.80	600.54	katil-terasa			
64	7507972.13	4699817.12	600.54	katil-terasa		Terasa	5.64
65	7507973.74	4699817.65	600.54	katil-terasa			
66	7507971.07	4699820.23	600.54	katil-terasa		Gjithsej:	104.28

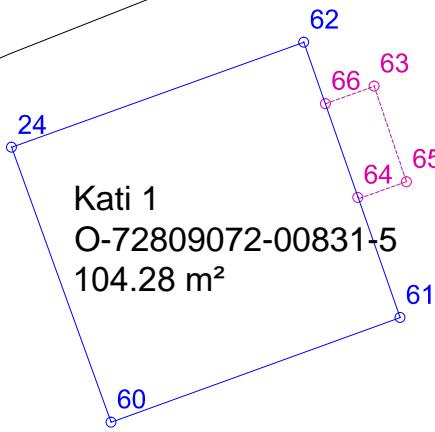**00831-5****Rr. "Maliq Hoxha"**Rilevoi / Snimio: LIRIDON SEJDIU
(emri dhe mbiemri i gjydetit/kompanisë/ ime i prezime geodeta/ kompanije)Aprovoi / Usvojio: _____
(emri dhe mbiemri i pësonit zyrtar/ ime i prezime sluzbeneg lica)Nr. i licencës / Br. licence: 140

V.V.

Nënshkrimi / Potpis: _____

Nënshkrimi / Potpis: _____

Data e rilevimit / Datum snimanja: 21.08.2025

Data e rilevimit / Datum snimanja: _____



Republika e Kosovës

Republika Kosova-Republic of Kosovo

Geveria e Kosovës- Vlada Kosova- Government of Kosovo

Ministria e Infrastrukturës dhe Ambientit/ Ministratvo Infrastrukture i Sredine/ Ministry of Infrastructure and Environment

AGJENCIA KADASTRALE E KOSOVËS/KOSOVSKA KATASTARSKA AGENCIJA/ KOSOVO CADASTRAL AGENCY

Komuna: Shtime
Numri i njësis kadastrale: 00831-2

Zona Kadastrale: Rashincë
Sistemi koordinat: KosovaRef01

Nr.	Y	X	H	D	Etazhi	Sqarim	Sipërfaqja (m²)
20	7507971.07	4699820.23	598.21	perdhese	Përdhesa	Përdhesa	130.68
51	7507972.19	4699817.10	598.21	perdhese			
52	7507968.49	4699824.66	598.21	perdhese			
53	7507959.74	4699821.39	598.21	perdhese			
54	7507970.35	4699822.26	598.21	perdhese			
55	7507972.67	4699820.80	598.21	perdhese			
56	7507973.54	4699813.16	598.21	perdhese			
57	7507973.74	4699817.65	598.21	perdhese			
58	7507969.42	4699821.94	598.21	perdhese			
59	7507963.98	4699809.70	598.21	perdhese			
Gjithsej:							130.68

Nr.	Y	X	H	D	Etazhi	Sqarim	Sipërfaqja (m²)			
24	7507960.69	4699818.78	600.54	kati1	Kati 1	Kati 1	98.65			
60	7507963.98	4699809.70	600.54	kati1						
61	7507973.53	4699813.15	600.54	kati1		Terasa				
62	7507970.35	4699822.25	600.54	kati1						
63	7507972.67	4699820.80	600.54	kati1-terasa						
64	7507972.13	4699817.12	600.54	kati1-terasa						
65	7507973.74	4699817.65	600.54	kati1-terasa	Gjithsej:					
66	7507971.07	4699820.23	600.54	kati1-terasa	104.28					

Gjeodeti / Kompania gjeodete e licencuar:	Liridon Sejdiu	Nënshkrimi dhe vula:	
Numri i licencës	140		



Zona kadastrale / Katastarska zona: Rashincë

Numri i lëndës / Broj predmeta:

Lloji i njësisë kadastrale / Vrsta katastarske jedinice : Shtëpi

Republika e Kosovës

Republika Kosova-Republic of Kosovo


Qeveria -Vlada-Government

Ministria e Mjedisit dhe Planifikimit Hapësinor /Ministarstvo Sredine i Prostornog Planiranja/Ministry of Environment and Spatial Planning

AGJENCIA KADASTRALE E KOSOVËS/KATASTARSKA AGECIJA KOSOVA/KOSOVA CADASTRAL AGENCY



Nr	Y	X	H	Kodi	Përshkrimi	Burimi
20	7507971.066	4699820.228	598.212	40	Shtëpi-Ndërtesë	PM
51	7507972.187	4699817.097	598.212	40	Shtëpi-Ndërtesë	PM
52	7507968.493	4699824.660	598.212	40	Shtëpi-Ndërtesë	PM
53	7507959.743	4699821.387	598.212	40	Shtëpi-Ndërtesë	PM
54	7507970.347	4699822.259	598.212	40	Shtëpi-Ndërtesë	PM
55	7507972.674	4699820.797	598.212	40	Shtëpi-Ndërtesë	PM
56	7507973.537	4699813.156	598.212	40	Shtëpi-Ndërtesë	PM
57	7507973.740	4699817.647	598.212	40	Shtëpi-Ndërtesë	PM
58	7507969.423	4699821.943	598.212	40	Shtëpi-Ndërtesë	PM
59	7507963.975	4699809.695	598.212	40	Shtëpi-Ndërtesë	PM

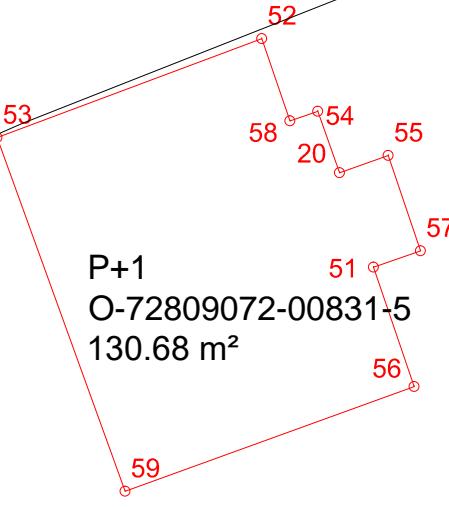
 598.033
 598.005

00831-5

Rr. "Maliq Hoxha"

Rilevoi / Snimio: **LIRIDON SEJDIU**
(emri dhe mbiemri i gjyqetit/kompanisë/ ime i prezime geodeta/ kompanije)Aprovoi / Usvojio: _____
(emri dhe mbiemri i pësonit zyrtar/ ime i prezime sluzbeneg lica)Nr. i licencës / Br. licence: **140**

V.V.

Nënshkrimi / Potpis: _____

Nënshkrimi / Potpis: _____

Data e rilevimit / Datum snimanja: **21.08.2025**

Data e rilevimit / Datum snimanja: _____



Republika e Kosovës

Republika Kosova-Republic of Kosovo

Qeveria e Kosovës- Vlada Kosova- Government of Kosovo

Ministria e Infrastrukturës dhe Ambientit/ Ministrastvo Infrastrukture i Sredine/ Ministry of Infrastructure and Environment
AGJENCIA KADASTRALE E KOSOVËS/KOSOVSKA KATASTARSKA AGENCIJA/ KOSOVO CADASTRAL AGENCY

Komuna: Shtime
Numri i njësis kadastrale: 00831-5

Zona Kadastrale: Rashincë
Sistemi koordinat: KosovaRef01

Nr	Y	X	H	Kodi	Përshkrimi	Burimi
20	7507971.066	4699820.228	598.212	40	Shtëpi-Ndërtesë	PM
51	7507972.187	4699817.097	598.212	40	Shtëpi-Ndërtesë	PM
52	7507968.493	4699824.660	598.212	40	Shtëpi-Ndërtesë	PM
53	7507959.743	4699821.387	598.212	40	Shtëpi-Ndërtesë	PM
54	7507970.347	4699822.259	598.212	40	Shtëpi-Ndërtesë	PM
55	7507972.674	4699820.797	598.212	40	Shtëpi-Ndërtesë	PM
56	7507973.537	4699813.156	598.212	40	Shtëpi-Ndërtesë	PM
57	7507973.740	4699817.647	598.212	40	Shtëpi-Ndërtesë	PM
58	7507969.423	4699821.943	598.212	40	Shtëpi-Ndërtesë	PM
59	7507963.975	4699809.695	598.212	40	Shtëpi-Ndërtesë	PM

Gjeodeti / Kompania gjeodete e licencuar:	Liridon Sejdiu	Nënshkrimi dhe vula:	
Numri i licencës	140		



Republika e Kosovës

Republika Kosova - Republic of Kosovo

Qeveria e Kosovës - Vlada Kosova - Government of Kosovo

Ministria e Infrastrukturës dhe Ambientit/ Ministrastvo Infrastrukture i Sredine/ Ministry of Infrastructure and Environment

AGJENCIA KADASTRALE E KOSOVËS/ KOSOVSKA KATASTARSKA AGENCIJA/ KOSOVA CADASTRAL AGENCY

R E G J I S T R I M I I NDERTESËS / SHTËPISË													
Nr	Komuna	Zona Kadastrale	Numri i ndërtesës (njësia)	Etazhiteti	Katet	Sipërfaqja e kateve [m ²]	Sipërfaqja e bazamentit [m ²]	Adresa e Njësisë	Vendi i quajtur	Shfrytëzimi i aktual	Pronari / Shfrytëzuesi Emri (Emri i prindit) Mbiemri	Numri përsoneal	Pjesa e Pronës
1	SHTIME	Rashincë	O-72809072-00831-5	P+11	Përdhesa	130.68	130.68	Rr. "Maliq Hoxha" Fsh. Rashincë-SHTIME	Rashitovit	Banim	Fadil Salihu	1004517926	1/1
					Kati 1	104.28							
					Gjithsej:	234.96							

Gjeodeti/kompania e licencuar: LIRIDON SEJDIU

Nr i licencës: 140

Nënshkrimi dhe vula:














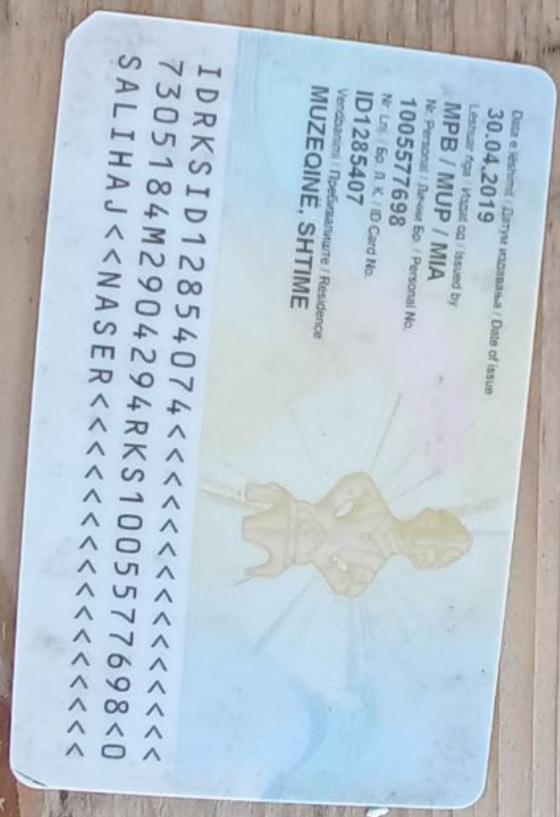

IDRKSID12854074<<<<<<<<<<
7305184M2904294RKS1005577698<0
SALIHA J << NASER <<<<<<<<















IDEA

044/414 525



IDEA **IDEA** **IDEA**

IDEA

044/414 525



IDEA

044/414 525

