

Nr	Y	X	H	Kodi	Përvkrimi	Burimi
35	7507816.332	4699749.903	598.933	40	Shtëpi-Ndërtesë	PM
36	7507820.427	4699740.985	598.933	40	Shtëpi-Ndërtesë	PM
38	7507806.951	4699745.625	598.933	40	Shtëpi-Ndërtesë	PM
39	7507811.022	4699736.696	598.933	40	Shtëpi-Ndërtesë	PM



Situacioni i terrenit

Zyra kadastrale kmunale / pëtinska katastarska kancelarija: _____ Shtime

Zona kadastrale / Katastarska zona: _____ Rashincë

Nr. i njësisë kadastrale / Br. katastarske jedinice : _____ 00831-2

Numri i lëndës / Broj predmeta: _____

Shkalla e zgjegimit / Razmera plana 1: _____ 250


Listë e koordinatave të pikave të matura:

Nr	Y	X	H	DSC
6	7507844.024	4699733.765	598.243	kyqje_uji
72	7507831.973	4699739.235	599.922	muze_fs2
76	7507827.573	4699757.498	598.724	muze_p4
77	7507844.391	4699732.123	598.320	muze_p5
78	7507804.298	4699726.152	598.541	muze_p6
35	7507816.332	4699749.903	598.933	perdhese
36	7507820.427	4699740.985	598.933	perdhese
38	7507806.951	4699745.625	598.933	perdhese
39	7507811.022	4699736.696	598.933	perdhese
5	7507845.426	4699733.174	598.278	pusetFeekkal
4	7507845.944	4699731.251	598.275	shtylElektrike
37	7507806.227	4699746.006	603.551	streha
45	7507817.356	4699751.081	603.500	streha
46	7507820.162	4699744.995	603.702	streha
47	7507817.776	4699747.500	605.993	streha
48	7507820.960	4699740.629	603.551	streha
49	7507810.814	4699735.947	603.551	streha

00831-2

Rr. "Maliq Hoxha"

muze_p6

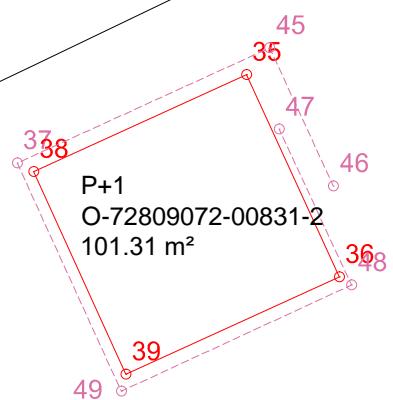

muze_p4

muze_fs2

muze_p5

599

Shpjegues:

Kufiri kadastral (nga SIKTK-G)

Rr.

Emri i rrugës

Ndërtesa në trajtim për legalizim

Pikë e objekteve fqinje

Ndërtesa tjera

Emri i rrugës

Aneks Ndërtimi

Pikë e strehëve

Shtyllë elektrike

Pikë e terasës

Pusetë e ujësjellësit

Pikë e objektit

Pusetë e ujërave të zezë

Pikë e murit

Strehët

Pikë e kulmit

Kyqje në rrymë

Pikë e objekteve fqinje

Rilevoi / Snimi: _____ LIRDON SEJDIU

(emri dhe mbiemri i gjedjetit/kompanisë/ ime i prezime gedeta/ kompanije)

Nr. i licencës / Br. licence: _____ 140

Data e rilevimit / Datum snimanja: _____ 21.08.2025

Nënshkrimi / Potpis: _____

V.V.

Nr	Y	X	H	Kodi	Përvkrimi	Burimi
35	7507816.332	4699749.903	598.933	40	Shtëpi-Ndërtesë	PM
36	7507820.427	4699740.985	598.933	40	Shtëpi-Ndërtesë	PM
38	7507806.951	4699745.625	598.933	40	Shtëpi-Ndërtesë	PM
39	7507811.022	4699736.696	598.933	40	Shtëpi-Ndërtesë	PM



Republika e Kosovës

Qeveria - Vlada



Ministria e Mjedisit dhe Planifikimit Hapësinor /Ministarstv Sredine i Prstrg Planiranja
AGJENCIJA KADASTRALE E KOSOVËS / KATASTARSKA AGENCJA KOSOVA

Situacioni i terrenit

Orto 2018

Zyra kadastrale kmunale / pëtinska katastarska kancelarija: _____ Shtime

Zona kadastrale / Katastarska zona: _____ Rashincë


Nr. i njësisë kadastrale / Br. katastarske jedinice : _____ 00831-2

Numri i lëndës / Broj predmeta: _____

Shkalla e zgjegimit / Razmera plana 1: _____ 250

Lista e koordinatave të pikave të matura:

Nr	Y	X	H	DSC
6	7507844.024	4699733.765	598.243	kyqje_uji
72	7507831.973	4699739.235	599.922	muze_fs2
76	7507827.573	4699757.498	598.724	muze_p4
77	7507844.391	4699732.123	598.320	muze_p5
78	7507804.298	4699726.152	598.541	muze_p6
35	7507816.332	4699749.903	598.933	perdhese
36	7507820.427	4699740.985	598.933	perdhese
38	7507806.951	4699745.625	598.933	perdhese
39	7507811.022	4699736.696	598.933	perdhese
5	7507845.426	4699733.174	598.278	pusetFeekkal
4	7507845.944	4699731.251	598.275	shtylElektrike
37	7507806.227	4699746.006	603.551	streha
45	7507817.356	4699751.081	603.500	streha
46	7507820.162	4699744.995	603.702	streha
47	7507817.776	4699747.500	605.993	streha
48	7507820.960	4699740.629	603.551	streha
49	7507810.814	4699735.947	603.551	streha

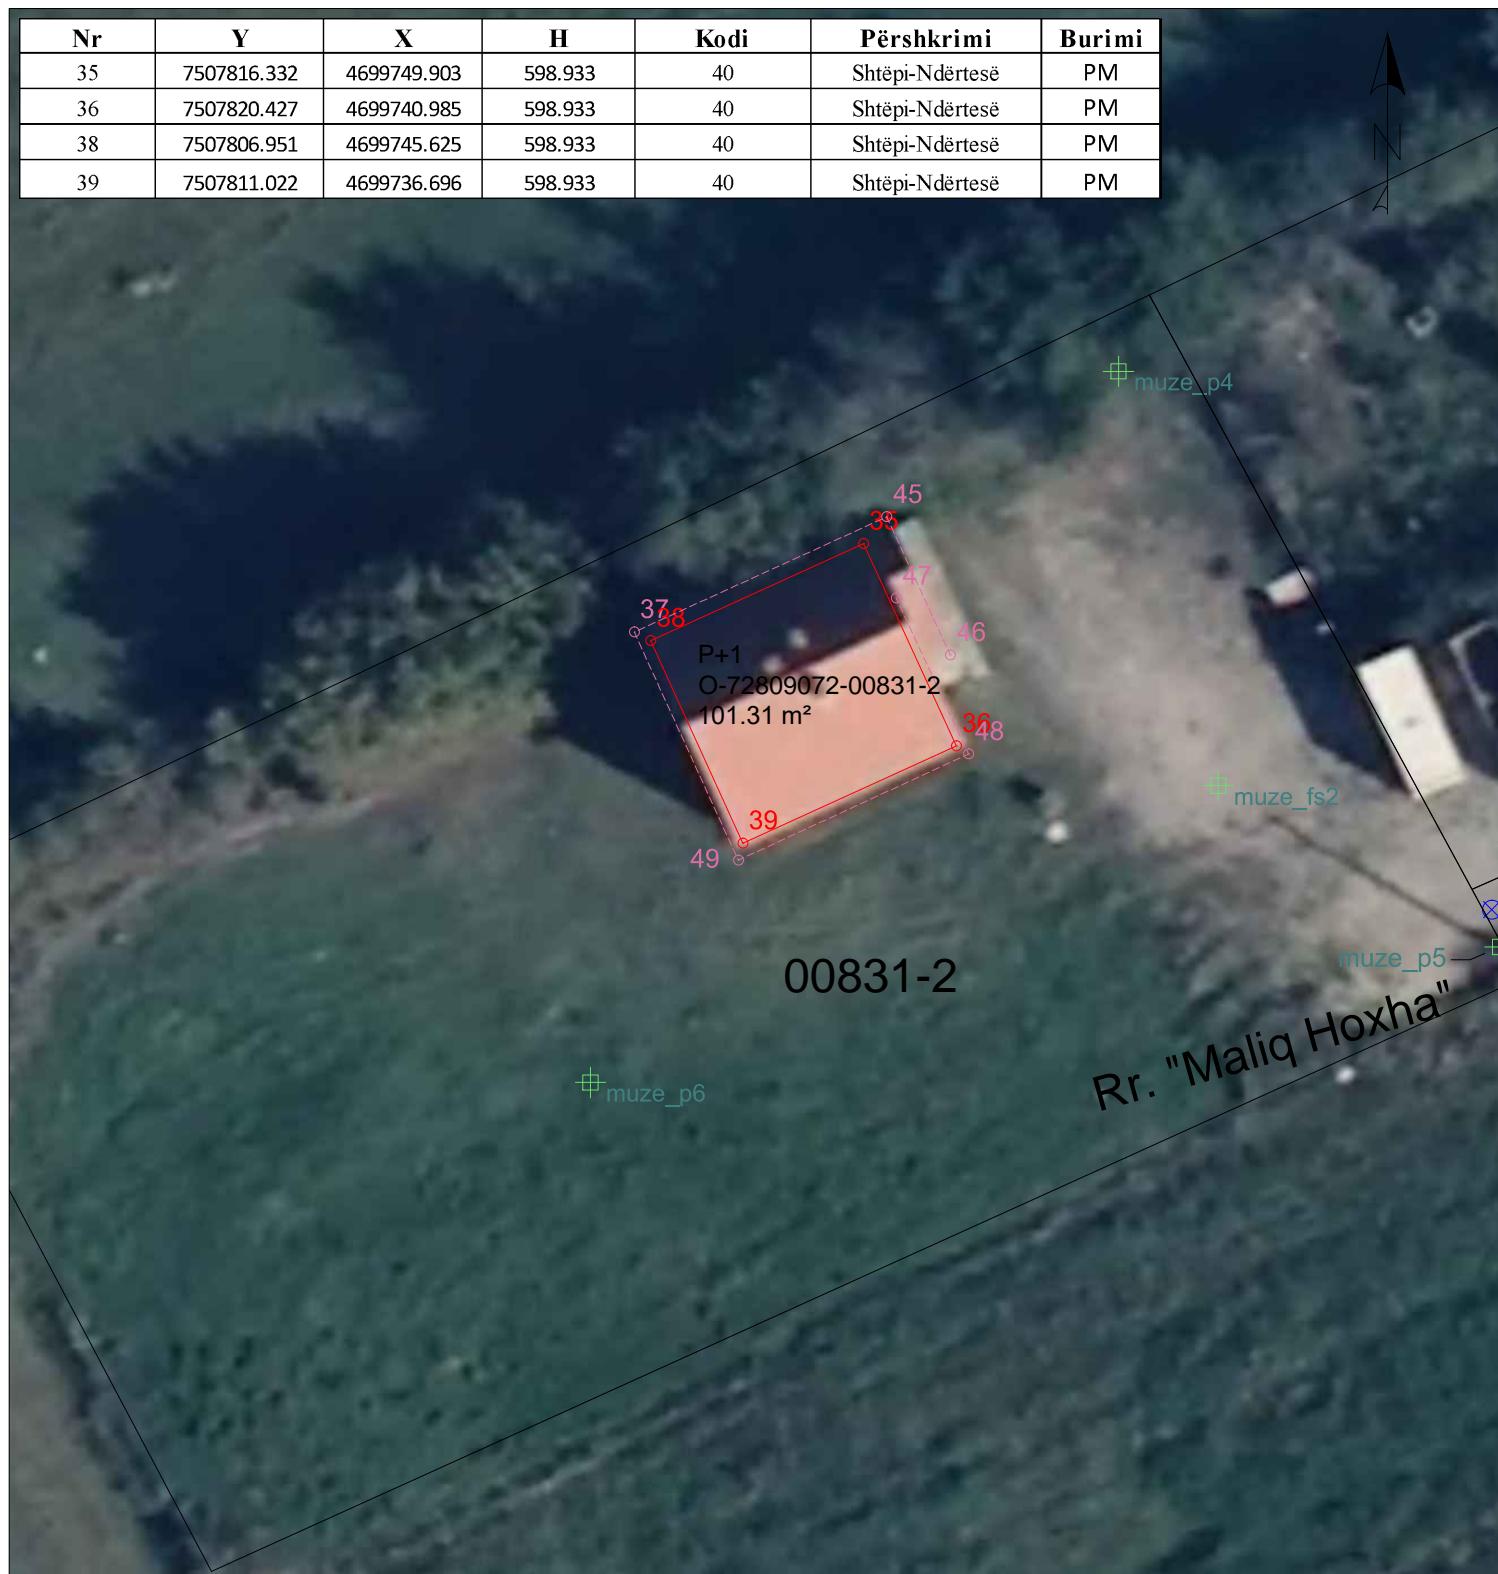

Shpjegues:

Kufiri kadastral (nga SIKTK-G)

Rr. Emri i rrugës

Ndërtesa në trajtim për legalizim

Pikë e terasës

Ndërtesa tjera

Pikë e strehëve

Aneks Ndërtimi

Pikë e objektit

81 Shtyllë elektrike

Pikë e murit

10 Pusetë e ujësjellësit

Pikë e kulmit

Pusetë e ujérave të zeza

Strehët

Strehët

Kyqje në rrymë

Rilevoi / Snimi: _____ LIRDON SEJDIU

(emri dhe mbiemri i gjedjetit/kompanisë/ ime i prezime gedeta/ kompanije)

Nr. i licencës / Br. licence: _____ 140

Data e rilevimit / Datum snimanja: _____ 21.08.2025

Nënshkrimi / Potpis: _____

V.V.



Republika e Kosovës
Republika Kosova-Republic of Kosovo
Qeveria e Kosovës- Vlada Kosova- Government of Kosovo
Ministria e Infrastrukturës dhe Ambientit/ Ministrastvo Infrastrukture i Sredine/ Ministry of Infrastructure and Environment
AGJENCIA KADASTRALE E KOSOVËS/KOSOVSKA KATASTARSKA AGENCIJA/ KOSOVO CADASTRAL AGENCY

Komuna: Shtime

Numri i njësis kadastrale: 00831-2

Zona Kadastrale: Rashincë

Sistemi koordinat: KosovaRef01

Nr	Y	X	H	Kodi	Përshkrimi	Burimi
35	7507816.332	4699749.903	598.933	40	Shtëpi-Ndërtesë	PM
36	7507820.427	4699740.985	598.933	40	Shtëpi-Ndërtesë	PM
38	7507806.951	4699745.625	598.933	40	Shtëpi-Ndërtesë	PM
39	7507811.022	4699736.696	598.933	40	Shtëpi-Ndërtesë	PM

Gjeodeti / Kompania gjeodete e licencuar:	Liridon Sejdiu	Nënshkrimi dhe vula:	
Numri i licencës	140		

Kérko | Rezultati i kërkimit | Shfaq Zgjedhur | Rezultatet | Shkarko | Ndhima

ParcelDetailId CadastreUnitId CadastreZoneId
 636712 P-72809072-00831-2 72809072

Vendos në objekt Zmadho në objekt

Numri i rezultateve: 1 (showing first 1)
Nga harta: 0

Detajet

ParcelDetailId:	636712	
CadastreUnitId:	P-72809072-00831-2	
CadastreZoneId:	72809072	
CadastreZoneCode:	72809072	
Geometry:	1	
Status:	1	
Sipërfaqja Grafike (m ²):	2119.3	

Raport

Lista e shtresës

- Ortofoto
 - Orthophoto2024Rural
 - Orthophoto2024Urban
 - Orthophoto2018Rural
 - Orthophoto2018Malore
 - Orthophoto2018Urban
 - Ortofoto 2015 UAV
 - Ortofoto 2012
 - Ortofoto 2009
 - Ortofoto 2004
- Hartat Topografike
 - Harta Topografike 1:250000
 - Harta Topografike 1:25000 (2015)
 - Nomenklatura
- Rindërtimi i Informacioneve Kadastrale
 - RIK_2025
- Modeli Dixhital i Terrenit
 - Modeli Dixhital i Terrenit
- Rilevimi
 - Indeksi i Ortofotove Rurale 2024
 - Indeksi i Ortofotove Urbane 2024
 - Indeks i Ortofotove 2018
- Rrjeti Rugor
 - Autostradë
 - Rrugë Nacionale
 - Rrugë Rajonale
- Njësia Administrative
 - Kufiri Shtetëror
 - Kufijtë dhe Emrat e Komunave
 - Zonë urbane
- Njësiet Kadastrale
 - Zonat Kadastrale
 - Parcelat
 - Numri parcelës
 - Ndërtesa
 - Numri ndërtesa
- Sistemi i Adresave
 - Rrugët

00157-2 00157-3 00830-0 00831-4 00831-1 00831-12 00831-11 00832-0 00822-0

Scale = 1 : 1000

Pozita: 7507779.819, 4699752.868

KosovaRef01


Copyright © Agjencja Kadastrale e Kosovës

Zyra kadastrale komunale / Opštinska katastarska kancelarija: ShtimeNr. i njësisë kadastrale / Br. katastarske jedinice : 00831-2Zona kadastrale / Katastarska zona: Rashincë

Numri i lëndës / Broj predmeta: _____

Lloji i njësisë kadastrale / Vrsta katastarske jedinice : ShtëpiShkalla e zvoglimit / Razmera plana 1: 250**Republika e Kosovës****Republika Kosova-Republic of Kosovo****Qeveria -Vlada-Government****Ministria e Mjedisit dhe Planifikimit Hapësinor /Ministarstvo Sredine i Prostornog Planiranja/Ministry of Environment and Spatial Planning**

AGJENCIA KADASTRALE E KOSOVËS/KATASTARSKA AGENCIJA KOSOVA/KOSOVA CADASTRAL AGENCY

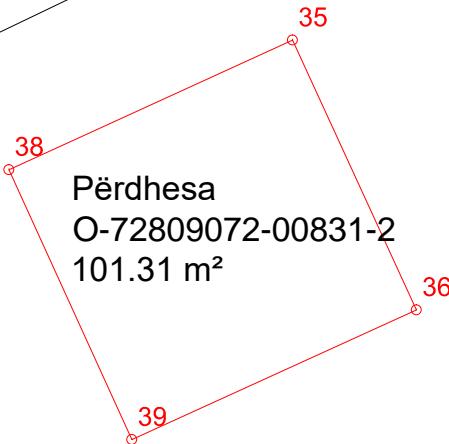**00831-2****Rr. "Maliq Hoxha"**

Nr.	Y	X	H	D	Etazhi	Sqarim	Sipë rfaqja (m ²)
35	7507816.33	4699749.90	598.93	perdhese	Përdhesa	Përdhesa	101.31
36	7507820.43	4699740.99	598.93	perdhese			
38	7507806.95	4699745.62	598.93	perdhese			
39	7507811.02	4699736.70	598.93	perdhese			
Gjithsej:							101.31

Rilevoi / Snimio: LIRIDON SEJDIU
(emri dhe mbiemri i gjydetit/kompanisë/ ime i prezime geodeta/ kompanije)Aprovoi / Usvojo: _____
(emri dhe mbiemri i pësonit zyrtar/ ime i prezime sluzbeneg lica)Nr. i licencës / Br. licence: 140

V.V.

Nënshkrimi / Potpis: _____

Nënshkrimi / Potpis: _____

Data e rilevimit / Datum snimanja: 21.08.2025

Data e rilevimit / Datum snimanja: _____

Zyra kadastrale komunale / Opštinska katastarska kancelarija: ShtimeNr. i njësisë kadastrale / Br. katastarske jedinice : 00831-2Zona kadastrale / Katastarska zona: Rashincë

Numri i lëndës / Broj predmeta: _____


Lloji i njësisë kadastrale / Vrsta katastarske jedinice : ShtëpiShkalla e zvoglimit / Razmera plana 1: 250**Republika e Kosovës**

Republika Kosova-Republic of Kosovo

Qeveria -Vlada-Government

Ministria e Mjedisit dhe Planifikimit Hapësinor /Ministarstvo Sredine i Prostornog Planiranja/Ministry of Environment and Spatial Planning

AGJENCIA KADASTRALE E KOSOVËS/KATASTARSKA AGENCIJA KOSOVA/KOSOVA CADASTRAL AGENCY

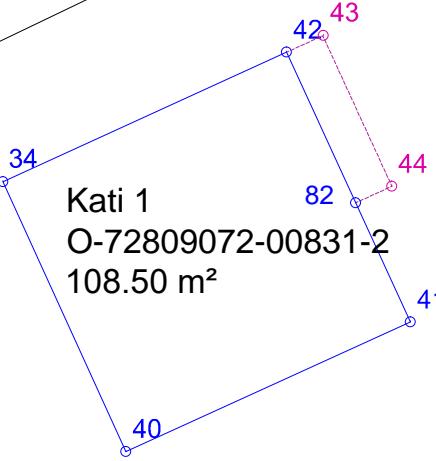**00831-2****Rr. "Maliq Hoxha"**

Nr.	Y	X	H	D	Etazhi	Sqarim	Sipërfaqja (m ²)
34	7507806.95	4699745.62	601.50	katil	Kati 1	Kati 1	101.31
40	7507811.02	4699736.70	601.50	katil			
41	7507820.43	4699740.99	601.50	katil		Terasa	7.19
42	7507816.33	4699749.90	601.50	katil			
82	7507818.62	4699744.93	601.50	katil		Gjithsej:	108.50
43	7507817.55	4699750.46	601.50	katil-terasa			
44	7507819.81	4699745.47	601.50	katil-terasa			

Rilevoi / Snimio: LIRIDON SEJDIU
(emri dhe mbiemri i gjydetit/kompanisë/ ime i prezime geodeta/ kompanije)Aprovoi / Usvojio: _____
(emri dhe mbiemri i pësonit zyrtar/ ime i prezime sluzbeneg lica)Nr. i licencës / Br. licence: 140

V.V.

Nënshkrimi / Potpis: _____

Nënshkrimi / Potpis: _____

Data e rilevimit / Datum snimanja: 21.08.2025

Data e rilevimit / Datum snimanja: _____



Republika e Kosovës

Republika Kosova-Republic of Kosovo

Qeveria e Kosovës- Vlada Kosova- Government of Kosovo

Ministria e Infrastrukturës dhe Ambientit/ Ministrastvo Infrastrukture i Sredine/ Ministry of Infrastructure and Environment

AGJENCIA KADASTRALE E KOSOVËS/KOSOVSKA KATASTARSKA AGENCIJA/ KOSOVO CADASTRAL AGENCY

Komuna: Shtime
Numri i njësis kadastrale: 00831-2

Zona Kadastrale: Rashincë
Sistemi koordinat: KosovaRef01

Nr.	Y	X	H	D	Etazhi	Sqarim	Sipërfaqja (m ²)
35	7507816.33	4699749.90	598.93	perdhese	Përdhesa	Përdhesa	101.31
36	7507820.43	4699740.99	598.93	perdhese			
38	7507806.95	4699745.62	598.93	perdhese		Gjithsej:	101.31
39	7507811.02	4699736.70	598.93	perdhese			

Nr.	Y	X	H	D	Etazhi	Sqarim	Sipërfaqja (m ²)
34	7507806.95	4699745.62	601.50	katil	Kati 1	Kati 1	101.31
40	7507811.02	4699736.70	601.50	katil			
41	7507820.43	4699740.99	601.50	katil		Terasa	7.19
42	7507816.33	4699749.90	601.50	katil			
82	7507818.62	4699744.93	601.50	katil			
43	7507817.55	4699750.46	601.50	katil-terasa			
44	7507819.81	4699745.47	601.50	katil-terasa		Gjithsej:	108.50

Gjeodeti / Kompania gjeodete e licencuar:	Liridon Sejdiu	Nënshkrimi dhe vula:	
Numri i licencës	140		



Zona kadastrale / Katastarska zona: _____ Rashincë _____

Numri i lëndës / Broj predmeta: _____

Lloji i njësisë kadastrale / Vrsta katastarske jedinice : Shtëpi _____


Republika e Kosovës

Republika Kosova-Republic of Kosovo

Qeveria -Vlada-Government

Ministria e Mjedisit dhe Planifikimit Hapësinor /Ministarstvo Sredine i Prostornog Planiranja/Ministry of Environment and Spatial Planning

AGJENCIA KADASTRALE E KOSOVËS/KATASTARSKA AGENCIJA KOSOVA/KOSOVA CADASTRAL AGENCY

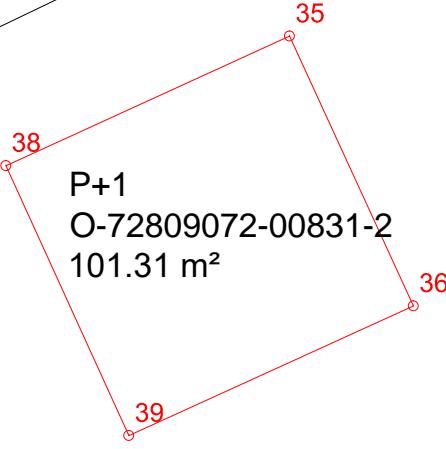

00831-2

Rr. "Maliq Hoxha"

Nr	Y	X	H	Kodi	Përshkrimi	Burimi
35	7507816.332	4699749.903	598.933	40	Shtëpi-Ndërtesë	PM
36	7507820.427	4699740.985	598.933	40	Shtëpi-Ndërtesë	PM
38	7507806.951	4699745.625	598.933	40	Shtëpi-Ndërtesë	PM
39	7507811.022	4699736.696	598.933	40	Shtëpi-Ndërtesë	PM

Rilevoi / Snimio: LIRIDON SEJDIU
(emri dhe mbiemri i gjydetit/kompanisë/ ime i prezime geodeta/ kompanije)Aprovoi / Usvojio: _____
(emri dhe mbiemri i përsorit zyrtar/ ime i prezime sluzbeneg lica)Nr. i licencës / Br. licence: 140

V.V.

Nënshkrimi / Potpis: _____

Nënshkrimi / Potpis: _____

Data e rilevimit / Datum snimanja: 21.08.2025

Data e rilevimit / Datum snimanja: _____



Republika e Kosovës
Republika Kosova-Republic of Kosovo
Qeveria e Kosovës- Vlada Kosova- Government of Kosovo
Ministria e Infrastrukturës dhe Ambientit/ Ministrastvo Infrastrukture i Sredine/ Ministry of Infrastructure and Environment
AGJENCIA KADASTRALE E KOSOVËS/KOSOVSKA KATASTARSKA AGENCIJA/ KOSOVO CADASTRAL AGENCY

Komuna: Shtime

Numri i njësis kadastrale: 00831-2

Zona Kadastrale: Rashincë

Sistemi koordinat: KosovaRef01

Nr	Y	X	H	Kodi	Përshkrimi	Burimi
35	7507816.332	4699749.903	598.933	40	Shtëpi-Ndërtesë	PM
36	7507820.427	4699740.985	598.933	40	Shtëpi-Ndërtesë	PM
38	7507806.951	4699745.625	598.933	40	Shtëpi-Ndërtesë	PM
39	7507811.022	4699736.696	598.933	40	Shtëpi-Ndërtesë	PM

Gjeodeti / Kompania gjeodete e licencuar:	Liridon Sejdiu	Nënshkrimi dhe vula:	
Numri i licencës	140		



Republika e Kosovës

Republika Kosova - Republic of Kosovo

Qeveria e Kosovës - Vlada Kosova - Government of Kosovo

Ministria e Infrastrukturës dhe Ambientit/ Ministrastvo Infrastrukture i Sredine/ Ministry of Infrastructure and Environment

AGJENCIA KADASTRALE E KOSOVËS/ KOSOVSKA KATASTARSKA AGENCIJA/ KOSOVA CADASTRAL AGENCY

R E G J I S T R I M I I NDERTESËS / SHTËPISË													
Nr	Komuna	Zona Kadastrale	Numri i ndërtesës (njësia)	Etazhiteti	Katet	Sipërfaqja e kateve [m ²]	Sipërfaqja e bazamentit [m ²]	Adresa e Njësisë	Vendi i quajtur	Shfrytëzimi i aktual	Pronari / Shfrytëzuesi Emri (Emri i prindit) Mbiemri	Numri përsoneal	Pjesa e Pronës
1	SHTIME	Rashincë	O-72809072-00831-2	P+1	Përdhesa	101.31	101.31	Rr. "Maliq Hoxha" Fsh. Rashincë- SHTIME	Rashitovit	Banim	Nebih Salihu	1030125009	1/1
					Kati 1	108.50							
					Gjithsej:	209.81							

Gjeodeti/kompania e licencuar: LIRIDON SEJDIU	Nr i licencës: 140	Nënshkrimi dhe vula:
---	--------------------	----------------------














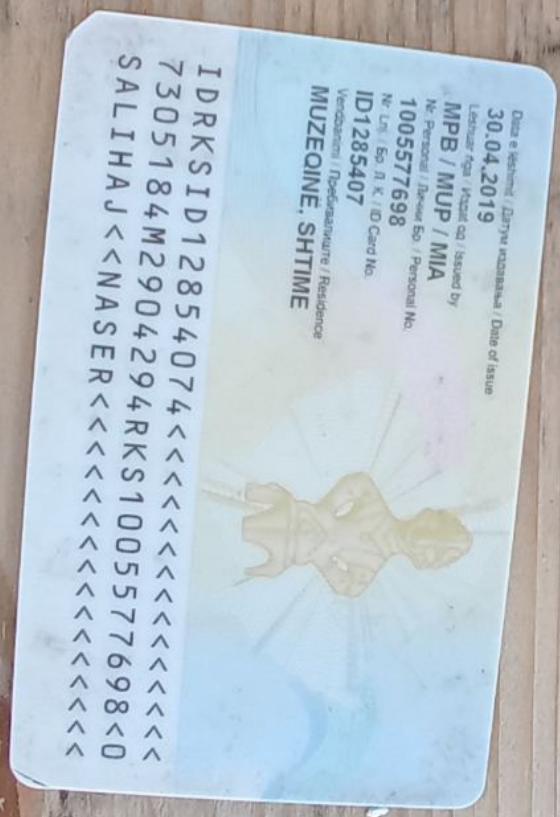

IDRKSID12854074<<<<<<<<<<
7305184M2904294RKS1005577698<0
SALIHA J << NASER <<<<<<<<















IDEA

044/414 525



IDEA **IDEA** **IDEA**


IDEA

044/414 525



IDEA

044/414 525

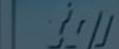

www.termogroup.com

