

Nr	Y	X	H	Kodi	Përshkrimi	Burimi
11	7508008.275	4699807.964	599.678	40	Shtëpi-Ndërtesë	PM
12	7508017.508	4699812.172	599.678	40	Shtëpi-Ndërtesë	PM
13	7508013.503	4699820.961	599.678	40	Shtëpi-Ndërtesë	PM
16	7508004.316	4699816.830	599.678	40	Shtëpi-Ndërtesë	PM



Republika e Kosovës

Qeveria - Vlada



Ministria e Mjedisit dhe Planifikimit Hapësinor /Ministarstv Sredine i Prstrg Planiranja
AGJENCIJA KADASTRALE E KOSOVËS / KATASTARSKA AGENCJA KOSOVA

Situacioni i terrenit

Zyra kadastrale kmunale / pëtinska katastarska kancelarija: _____ Shtime

Zona kadastrale / Katastarska zona: _____ Rashincë

Nr. i njësisë kadastrale / Br. katastarske jedinice : _____ 00831-9

Numri i lëndës / Broj predmeta: _____

Shkalla e zvoglimit / Razmera plana 1: _____ 250

Listë e koordinatave të pikave të matura:

Nr	Y	X	H	DSC
70	7507989.536	4699808.230	599.720	muz_fs3
79	7507990.624	4699829.042	598.299	muze_p7
80	7508027.453	4699836.996	598.087	muze_p8
81	7507966.986	4699786.056	598.045	muze_p9
11	7508008.275	4699807.964	599.678	perdhese
12	7508017.508	4699812.172	599.678	perdhese
13	7508013.503	4699820.961	599.678	perdhese
16	7508004.316	4699816.830	599.678	perdhese
8	7507957.699	4699783.112	598.031	pusetFeekkal
10	7508004.300	4699803.764	598.085	pusetFeekkal
7	7507963.634	4699783.136	597.937	shtyElektrike
9	7508000.545	4699799.346	598.059	shtyElektrike
14	7508036.450	4699815.493	598.084	shtyElektrike
15	7507998.199	4699834.710	598.376	shtyElektrike

Shpjegues:

— Kufiri kadastral (nga SIKTK-G)

Pikë e objekteve fqinje

Ndërtesa në trajtim për legalizim

Rr. Emri i rrugës

Ndërtesa tjera

Pikë e rrejtës gjeodezike

Aneks Ndërtimi

Pikë e strehëve

16 Shtyllë elektrike

Pikë e terasës

● Pusetë e ujësjellësit

Pikë e objektit

○ Pusetë e ujërave të zeza

Pikë e murit

— Strehët

Pikë e kulmit

11 Kyqje në rrymë

Rilevoi / Snimi: LIRIDON SEJDIU


(emri dhe mbiemri i gjedjetit/kompanisë / ime i prezime gedeta/ kompanije)

Nr. i licencës / Br. licence: 140

Data e rilevimit / Datum snimanja: 21.08.2025

Nënshkrimi / Potpis: _____

V.V.

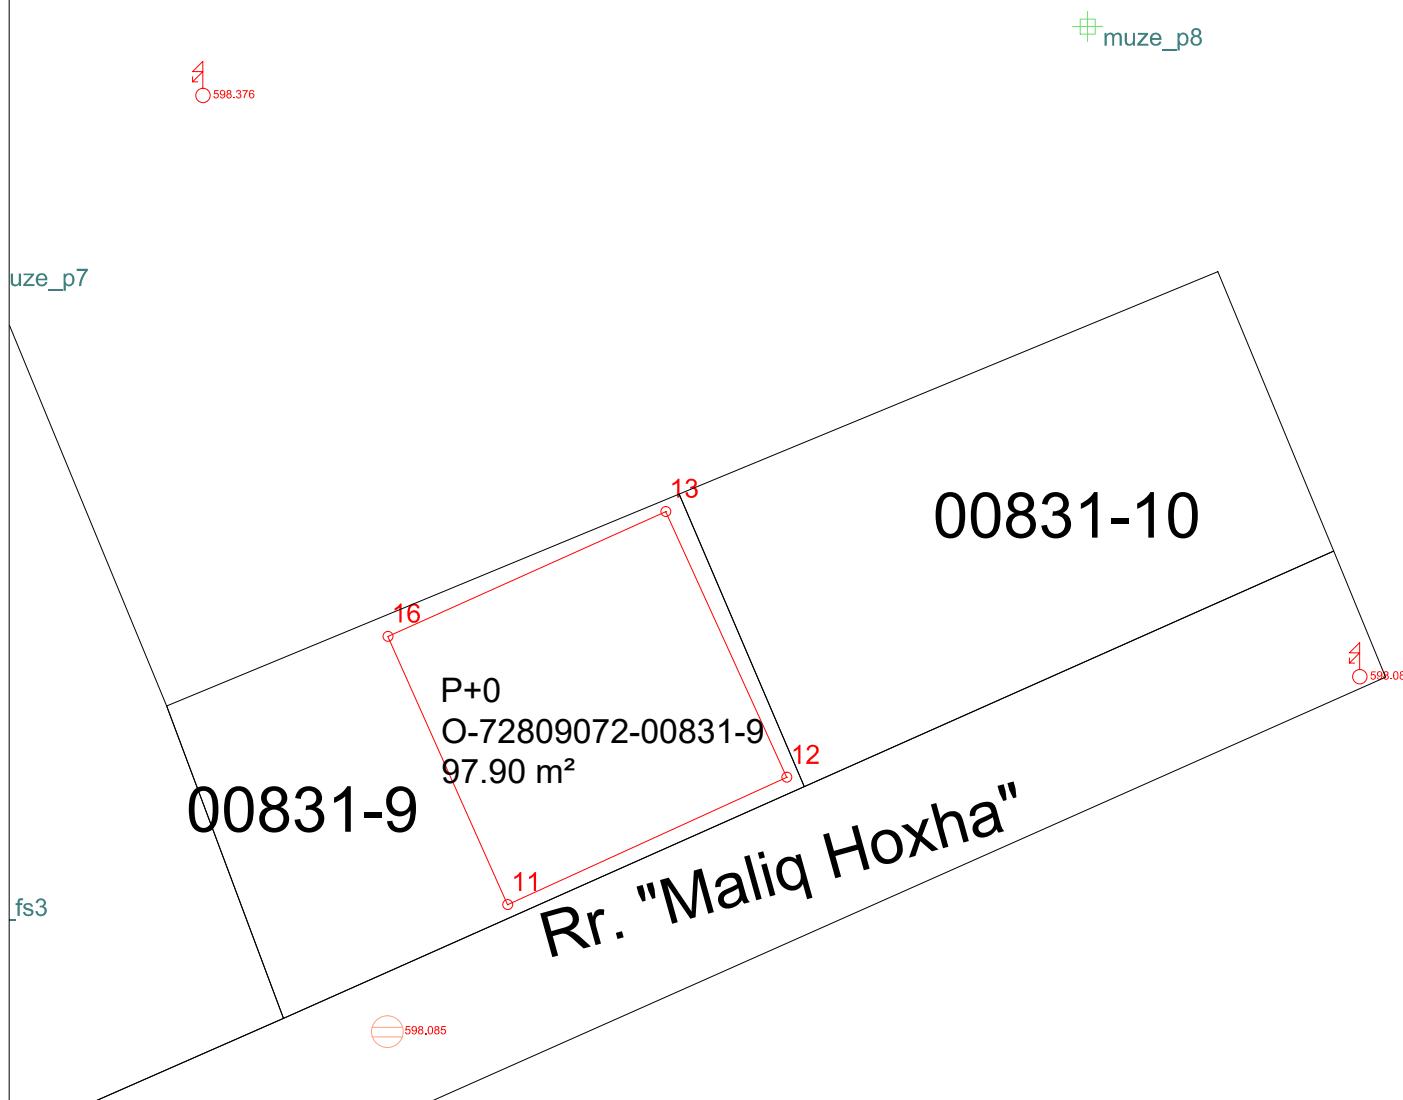

Nr	Y	X	H	Kodi	Përshkrimi	Burimi
11	7508008.275	4699807.964	599.678	40	Shtëpi-Ndërtesë	PM
12	7508017.508	4699812.172	599.678	40	Shtëpi-Ndërtesë	PM
13	7508013.503	4699820.961	599.678	40	Shtëpi-Ndërtesë	PM
16	7508004.316	4699816.830	599.678	40	Shtëpi-Ndërtesë	PM



Republika e Kosovës
Qeveria - Vlada
Ministria e Mjedisit dhe Planifikimit Hapësinor /Ministarstv Sredine i Prstrig Planiranja
AGJENCIJA KADASTRALE E KOSOVËS / KATASTARSKA AGJENCIJA KOSOVA



Situacioni i terrenit

Orto 2018

Zyra kadastrale kmunale / pëtinska katastarska kancelarija: _____ Shtime

Zona kadastrale / Katastarska zona: _____ Rashinçë

Nr. i njësisë kadastrale / Br. katastarske jedinice : _____ 00831-9

Numri i lëndës / Broj predmeta: _____

Shkalla e zvoglimit / Razmera plana 1: _____ 250

Lista e koordinatave të pikave të matura:

Nr	Y	X	H	DSC
70	7507989.536	4699808.230	599.720	muz_fs3
79	7507990.624	4699829.042	598.299	muze_p7
80	7508027.453	4699836.996	598.087	muze_p8
81	7507966.986	4699786.056	598.045	muze_p9
11	7508008.275	4699807.964	599.678	perdhese
12	7508017.508	4699812.172	599.678	perdhese
13	7508013.503	4699820.961	599.678	perdhese
16	7508004.316	4699816.830	599.678	perdhese
8	7507957.699	4699783.112	598.031	pusetFeekkal
10	7508004.300	4699803.764	598.085	pusetFeekkal
7	7507963.634	4699783.136	597.937	shtylElektrike
9	7508000.545	4699799.346	598.059	shtylElektrike
14	7508036.450	4699815.493	598.084	shtylElektrike
15	7507998.199	4699834.710	598.376	shtylElektrike

Shpjegues:

Kufiri kadastral (nga SIKTK-G)

Rr. Emri i rrugës

Ndërtesa në trajtim për legalizim

Pikë e rrejtës gjeodezike

Ndërtesa tjera

Pikë e strehëve

Aneks Ndërtimi

Pikë e terasës

Shtyllë elektrike

Pikë e objektit

Pusetë e ujësjellësit

Pikë e murit

Pusetë e ujërave të zeza

Pikë e kulmit

Strehët

Kyqje në rrymë

LIRIDON SEJDIU

(emri dhe mbiemri i gjedjetit/kompanisë/ ime i prezime gedeta/ kompanije)

Nr. i licencës / Br. licence: _____ 140

Data e rilevimit / Datum snimanja: _____ 21.08.2025

Nënshkrimi / Potpis: _____

V.V.



Republika e Kosovës
Republika Kosova-Republic of Kosovo
Qeveria e Kosovës- Vlada Kosova- Government of Kosovo
Ministria e Infrastrukturës dhe Ambientit/ Ministrastvo Infrastrukture i Sredine/ Ministry of Infrastructure and Environment
AGJENCIA KADASTRALE E KOSOVËS/KOSOVSKA KATASTARSKA AGENCIJA/ KOSOVO CADASTRAL AGENCY

Komuna: Shtime

Numri i njësis kadastrale: 00831-9

Zona Kadastrale: Rashincë

Sistemi koordinat: KosovaRef01

Nr	Y	X	H	Kodi	Përshkrimi	Burimi
11	7508008.275	4699807.964	599.678	40	Shtëpi-Ndërtesë	PM
12	7508017.508	4699812.172	599.678	40	Shtëpi-Ndërtesë	PM
13	7508013.503	4699820.961	599.678	40	Shtëpi-Ndërtesë	PM
16	7508004.316	4699816.830	599.678	40	Shtëpi-Ndërtesë	PM

Gjeodeti / Kompania gjeodete e licencuar:	Liridon Sejdiu	Nënshkrimi dhe vula:	
Numri i licencës	140		

Kërko

Rezultati i kërkimit

Shfaq Të gjitha Rezultatet Shkarko

ParcelDetailId CadastreUnitId CadastreZoneId Ga
636850 P-72809072-00... 72809072 72

Vendos në objekt Zmadho në objekt

Numri i rezultateve: 1 (showing first 1)
Nga harta: 1

Detajet

ParcelDetailId: 636850
CadastreUnitId: P-72809072-00831-9
CadastreZoneId: 72809072
CadastreZoneCode: 72809072
Geometry:
Status: 1
Sipërfaqja Grafike (m²): 200.0

Raport

Lista e shtresës Ndhima

- Ortofoto
 - Orthophoto2024Rural
 - Orthophoto2024Urban
 - Orthophoto2018Rural
 - Orthophoto2018Malore
 - Orthophoto2018Urban
 - Orthofoto 2015 UAV
 - Orthofoto 2012
 - Orthofoto 2009
 - Orthofoto 2004
- Hartat Topografike
 - Harta Topografike 1:250000
 - Harta Topografike 1:25000 (2015)
 - Nomenklatura
- Rindërtimi i Informacioneve Kadastrale
 - RIK_2025
- Modeli Dixhitali i Terrenit
 - Modeli Dixhitali i Terrenit
- Rilevimi
 - Indexi i Ortofotove Rurale 2024
 - Indexi i Ortofotove Urbane 2024
 - Indexi i Ortofotove 2018
- Rrjeti Rrugor
 - Autostradë
 - Rrugë Nacionale
 - Rrugë Rajonale
- Njësi Administrative
 - Kufiri Shtetëror
 - Kufijtë dhe Emrat e Komunave
 - Zonë urbane
- Njësitet Kadastrale
 - Zonat Kadastrale
 - Parcelat
 - Numri parcelës
 - Ndërtesa
 - Numri ndërtesës
- Sistemi i Adresave
 - Rrugët

1 : 1000

Auto Shfaq këshillat

Kërko

00143-3

00143-1

00143-5

00143-4

00142-0

00828-0

00829-0

00831-6

00831-8

00831-10

Rashincë

00831-9

00831-3

00831-4

00831-1

00831-11

00831-12

00831-13

00986-0


Scale = 1 : 1000

Pozita: 7507999.710, 4699841.15

KosovaRef01



598.376

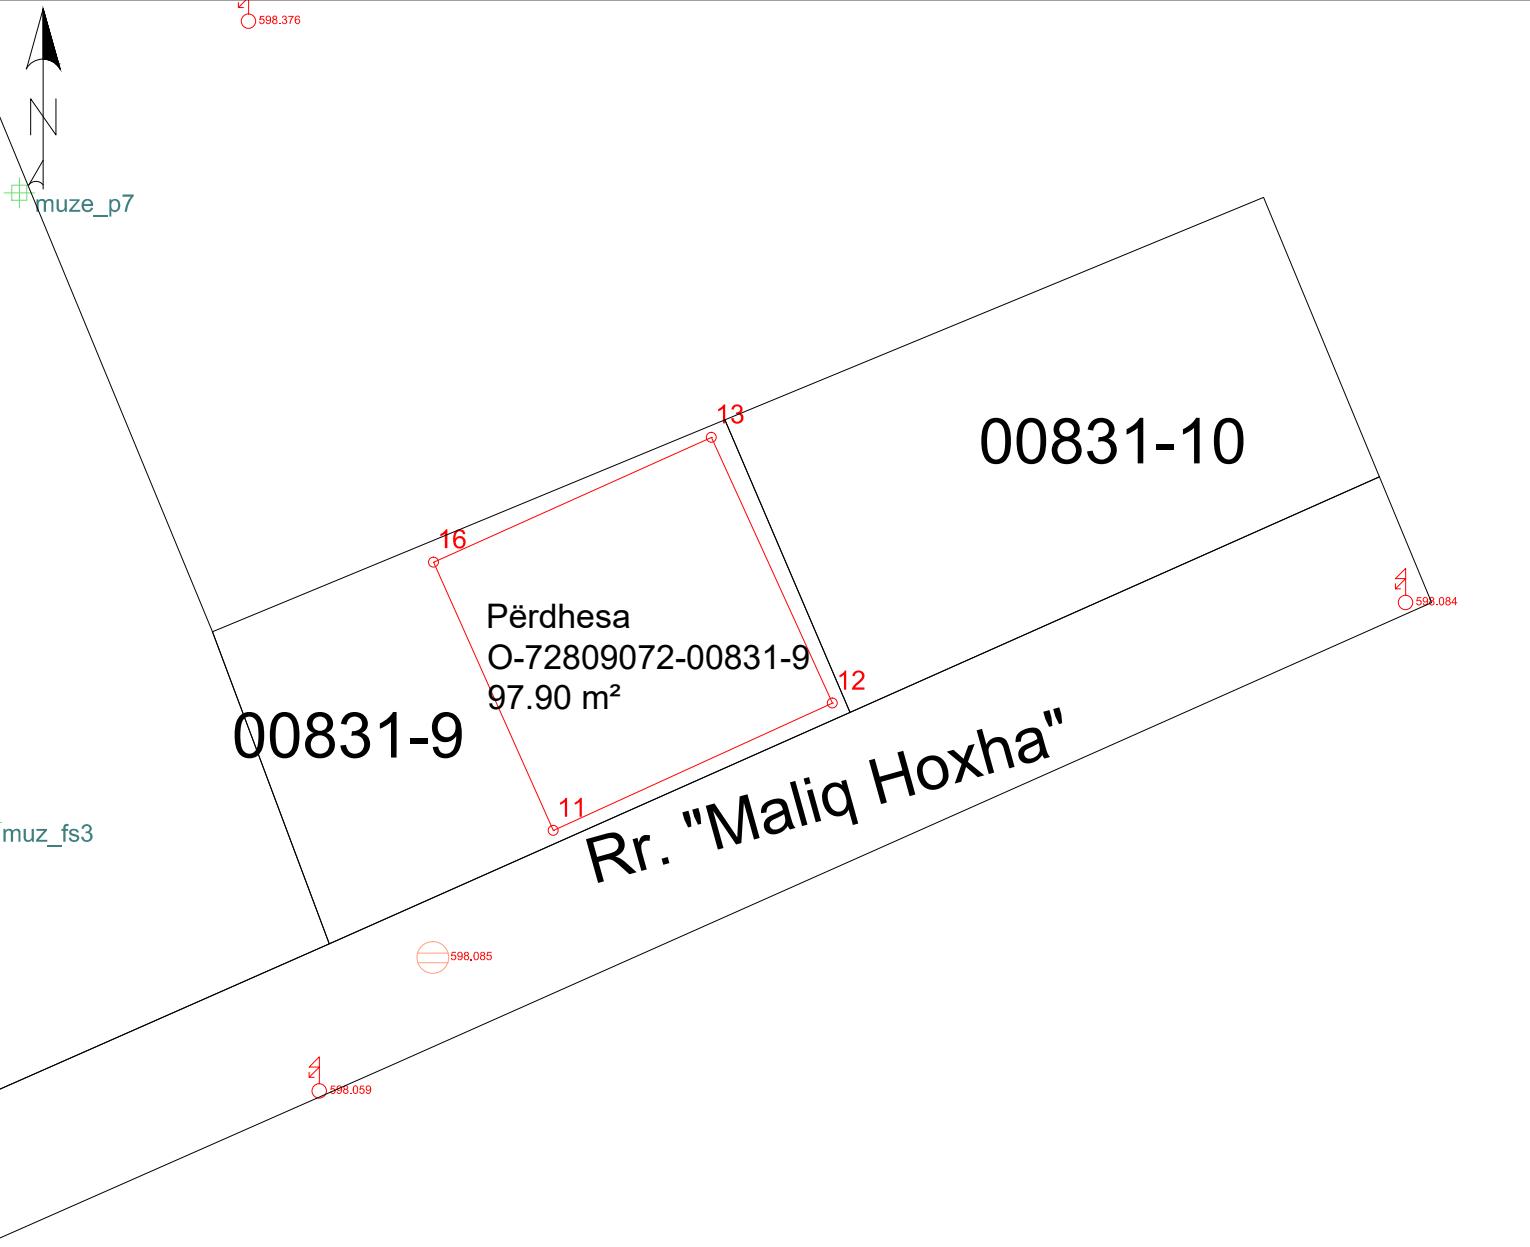

Nr.	Y	X	H	D	Etazhi	Sqarim	Sipërfaqja (m ²)
11	7508008.28	4699807.96	599.68	perdhese	Përdhesa	Përdhesa	97.90
12	7508017.51	4699812.17	599.68	perdhese			
13	7508013.50	4699820.96	599.68	perdhese			
16	7508004.32	4699816.83	599.68	perdhese		Gjithsej:	97.90

 Rilevoi / Snimio: LIRIDON SEJDIU
 (emri dhe mbiemri i gjykozit/kompanisë/ ime i prezime geodeta/ kompanije)

 Aprovoi / Usvojio: _____
 (emri dhe mbiemri i pësonit zyrtar/ ime i prezime sluzbeneg lica)
Nr. i licencës / Br. licence: 140

V.V.

Nënshkrimi / Potpis: _____

Nënshkrimi / Potpis: _____

Data e rilevimit / Datum snimanja: 21.08.2025

Data e rilevimit / Datum snimanja: _____



Republika e Kosovës

Republika Kosova-Republic of Kosovo

Qeveria e Kosovës- Vlada Kosova- Government of Kosovo

Ministria e Infrastrukturës dhe Ambientit/ Ministrastvo Infrastrukture i Sredine/ Ministry of Infrastructure and Environment

AGJENCIA KADASTRALE E KOSOVËS/KOSOVSKA KATASTARSKA AGENCIJA/ KOSOVO CADASTRAL AGENCY

Komuna: Shtime
Numri i njësis kadastrale: 00831-2

Zona Kadastrale: Rashincë
Sistemi koordinat: KosovaRef01

Nr.	Y	X	H	D	Etazhi	Sqarim	Sipërfaqja (m ²)
11	7508008.28	4699807.96	599.68	perdhese	Përdhesa	Përdhesa	97.90
12	7508017.51	4699812.17	599.68	perdhese			
13	7508013.50	4699820.96	599.68	perdhese		Gjithsej:	
16	7508004.32	4699816.83	599.68	perdhese		97.90	

Gjeodeti / Kompania gjeodete e licencuar:	Liridon Sejdiu	Nënshkrimi dhe vula:	
Numri i licencës	140		



Zona kadastrale / Katastarska zona: Rashincë

Numri i lëndës / Broj predmeta: _____

Lloji i njësisë kadastrale / Vrsta katastarske jedinice : Shtëpi

Republika e Kosovës

Republika Kosova-Republic of Kosovo

Qeveria -Vlada-Government

Ministria e Mjedisit dhe Planifikimit Hapësinor /Ministarstvo Sredine i Prostornog Planiranja/Ministry of Environment and Spatial Planning

AGJENCIA KADASTRALE E KOSOVËS/KATASTARSKA AGECIJA KOSOVA/KOSOVA CADASTRAL AGENCY

598.376

598.084

598.085

598.059

00831-9

00831-10

Rr. "Maliq Hoxha"

P+0
O-72809072-00831-9
97.90 m²


16

13

12

11

1

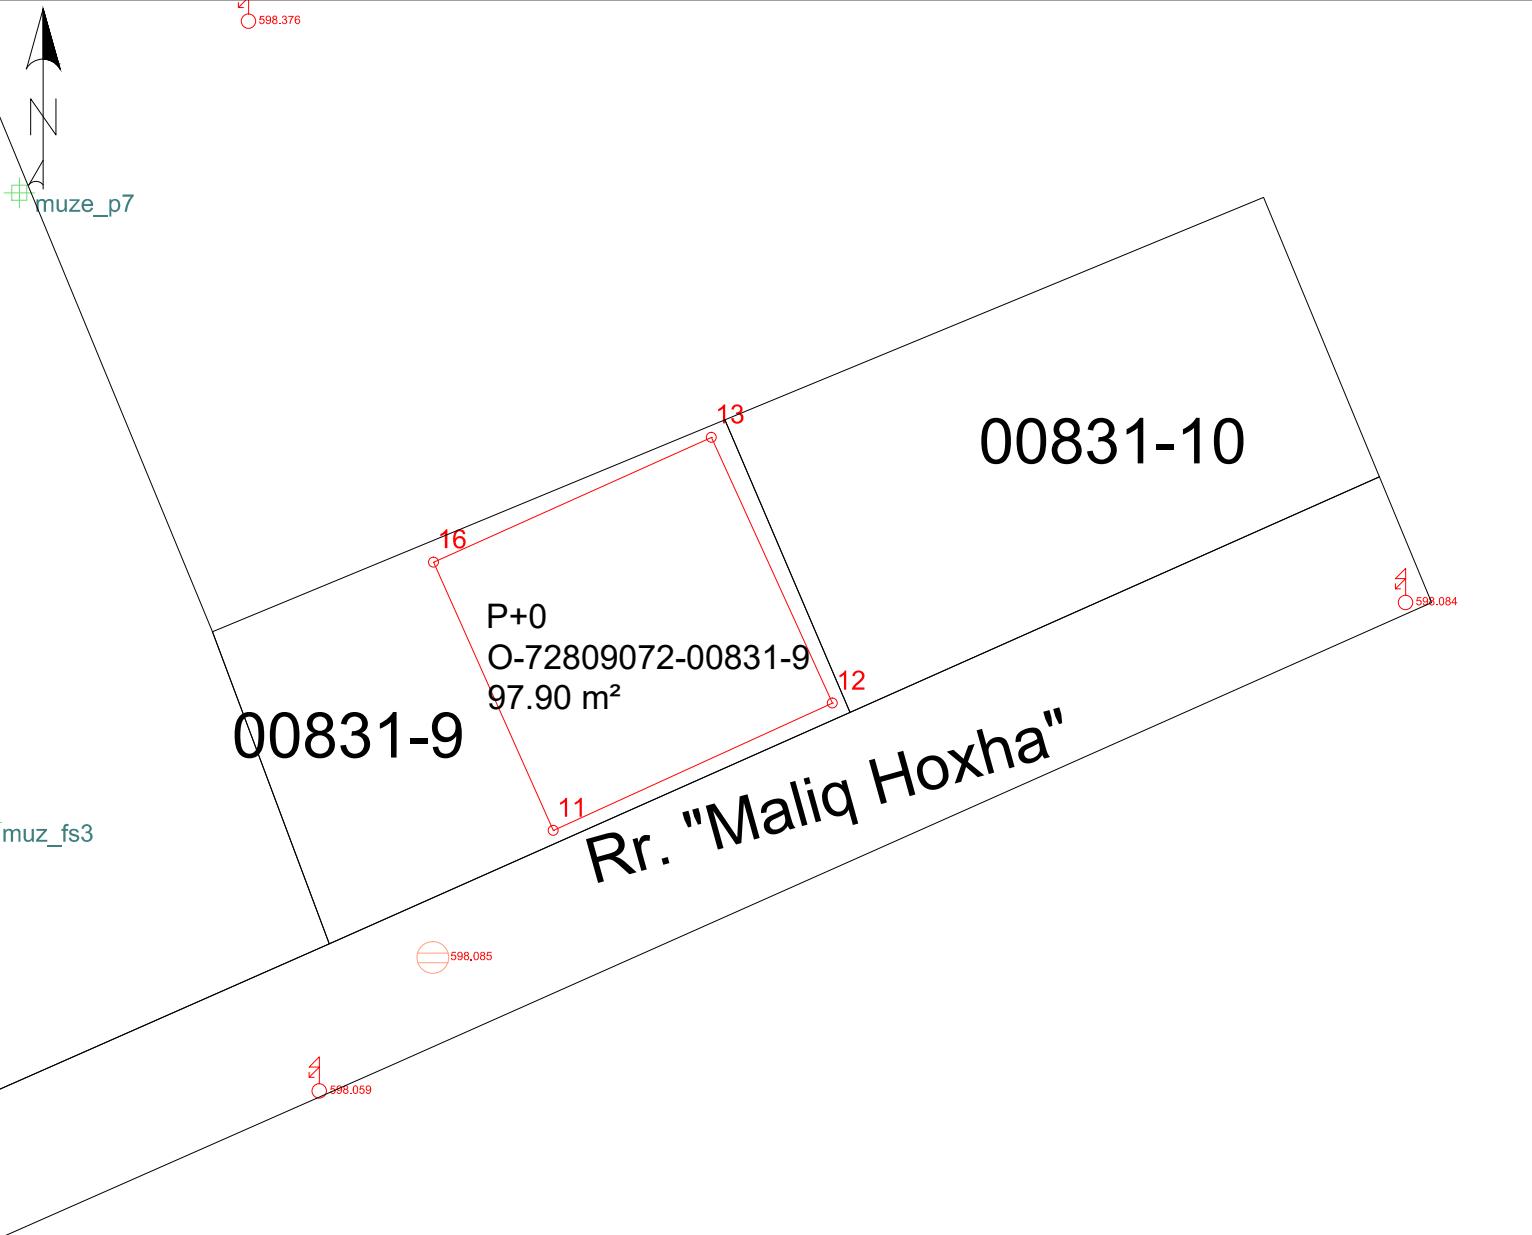

Nr	Y	X	H	Kodi	Përshkrimi	Burimi
11	7508008.275	4699807.964	599.678	40	Shtëpi-Ndërtesë	PM
12	7508017.508	4699812.172	599.678	40	Shtëpi-Ndërtesë	PM
13	7508013.503	4699820.961	599.678	40	Shtëpi-Ndërtesë	PM
16	7508004.316	4699816.830	599.678	40	Shtëpi-Ndërtesë	PM

Rilevoi / Snimio: LIRIDON SEJDIU
(emri dhe mbiemri i gjydetit/kompanisë/ ime i prezime geodeta/ kompanije)Aprovoi / Usvojio: _____
(emri dhe mbiemri i pësonit zyrtar/ ime i prezime sluzbeneg lica)

Nr. i licencës / Br. licence: 140

V.V.

Nënshkrimi / Potpis: _____

Nënshkrimi / Potpis: _____

Data e rilevimit / Datum snimanja: 21.08.2025

Data e rilevimit / Datum snimanja: _____



Republika e Kosovës
Republika Kosova-Republic of Kosovo
Qeveria e Kosovës- Vlada Kosova- Government of Kosovo
Ministria e Infrastrukturës dhe Ambientit/ Ministrastvo Infrastrukture i Sredine/ Ministry of Infrastructure and Environment
AGJENCIA KADASTRALE E KOSOVËS/KOSOVSKA KATASTARSKA AGENCIJA/ KOSOVO CADASTRAL AGENCY

Komuna: Shtime

Numri i njësis kadastrale: 00831-9

Zona Kadastrale: Rashincë

Sistemi koordinat: KosovaRef01

Nr	Y	X	H	Kodi	Përshkrimi	Burimi
11	7508008.275	4699807.964	599.678	40	Shtëpi-Ndërtesë	PM
12	7508017.508	4699812.172	599.678	40	Shtëpi-Ndërtesë	PM
13	7508013.503	4699820.961	599.678	40	Shtëpi-Ndërtesë	PM
16	7508004.316	4699816.830	599.678	40	Shtëpi-Ndërtesë	PM

Gjeodeti / Kompania gjeodete e licencuar:	Liridon Sejdiu	Nënshkrimi dhe vula:	
Numri i licencës	140		



Republika e Kosovës

Republika Kosova - Republic of Kosovo

Qeveria e Kosovës - Vlada Kosova - Government of Kosovo

Ministria e Infrastrukturës dhe Ambientit/ Ministrastvo Infrastrukture i Sredine/ Ministry of Infrastructure and Environment

AGJENCIA KADASTRALE E KOSOVËS/ KOSOVSKA KATASTARSKA AGENCIJA/ KOSOVA CADASTRAL AGENCY


R E G J I S T R I M I I N DERTESËS / SHTËPISË													
Nr	Komuna	Zona Kadastrale	Numri i ndërtesës (njësia)	Etazhitëti	Katet	Sipërfaqja e kateve [m ²]	Sipërfaqja e bazamentit [m ²]	Adresa e Njësisë	Vendi i quajtur	Shfrytëzimi i aktual	Pronari / Shfrytëzuesi Emri (Emri i prindit) Mbiemri	Numri përsnal	Pjesa e Pronës
1	SHTIME	Rashincë	O-72809072-00831-9	P+0	Përdhesa Gjithsej:	97.90 97.90	97.9	Rr. "Maliq Hoxha" Fsh. Rashincë-SHTIME	TËRBESH	Banim	Bedri (Nazif) Salihaj	1004963209	1/1

Gjeodeti/kompania e licencuar: LIRIDON SEJDIU	Nr i licencës: 140	Nënshkrimi dhe vula:
---	--------------------	----------------------



IDEA


044/414 525

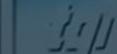

1



www.idealihaj.com

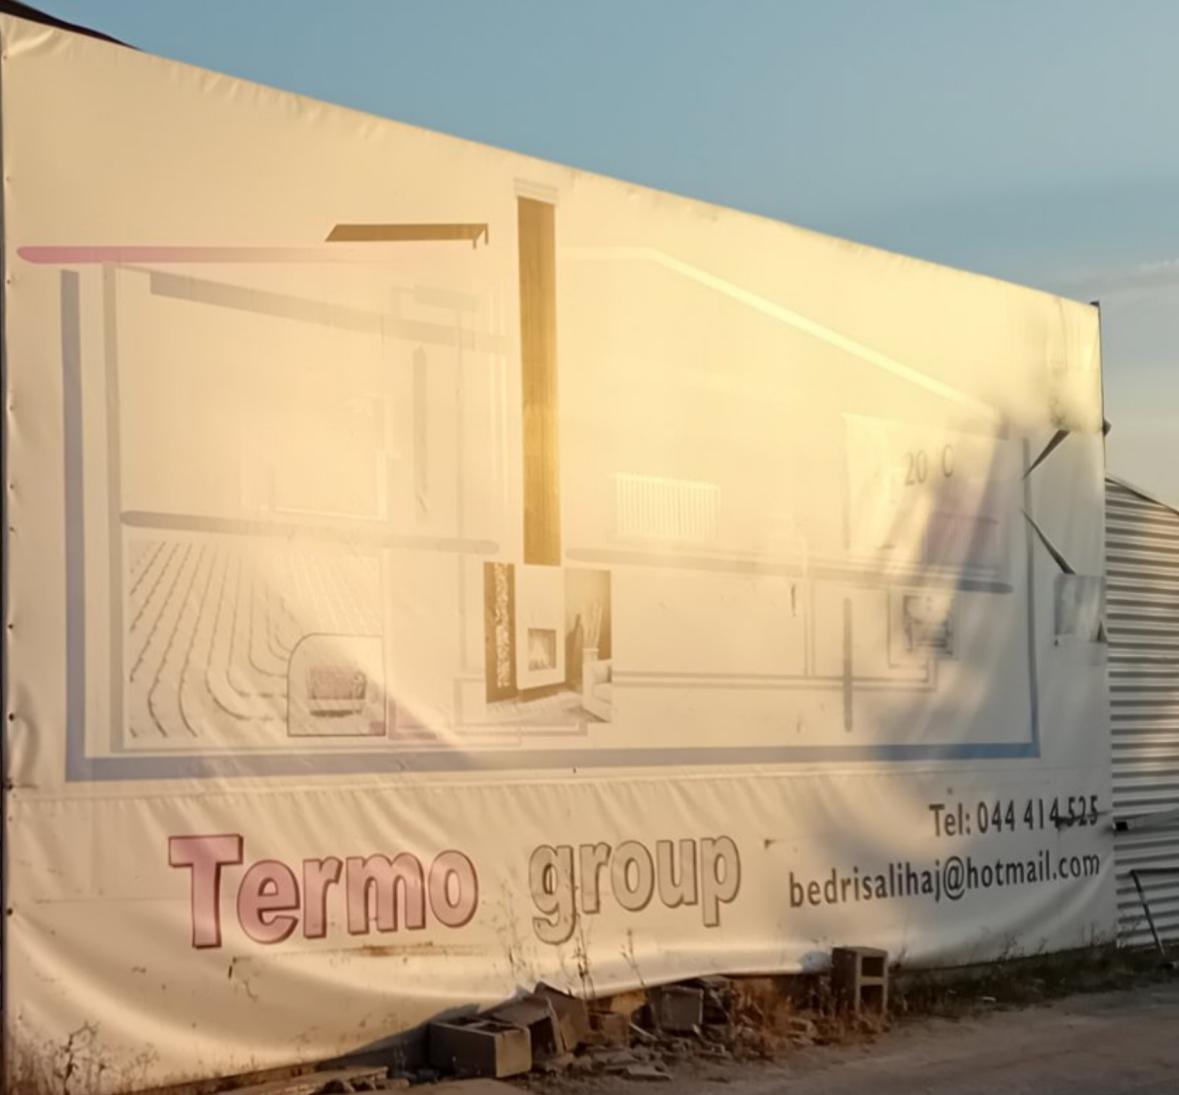

IDEA

IDEA

044/414 525



www.idealabvoda.com