


Nr	Y	X	H	Kodi	Përshkrimi	Burimi
20	7507919.544	4699799.530	598.429	40	Shtëpi-Ndërtesë	PM
22	7507917.736	4699799.301	598.429	40	Shtëpi-Ndërtesë	PM
53	7507918.823	4699799.828	598.429	40	Shtëpi-Ndërtesë	PM
82	7507919.815	4699798.965	598.316	40	Shtëpi-Ndërtesë	PM
83	7507921.174	4699796.065	598.429	40	Shtëpi-Ndërtesë	PM
84	7507921.437	4699795.498	598.276	40	Shtëpi-Ndërtesë	PM
85	7507921.216	4699794.751	598.268	40	Shtëpi-Ndërtesë	PM
86	7507920.159	4699794.259	598.286	40	Shtëpi-Ndërtesë	PM
87	7507921.675	4699791.008	598.278	40	Shtëpi-Ndërtesë	PM
88	7507907.971	4699795.466	598.429	40	Shtëpi-Ndërtesë	PM
89	7507912.212	4699786.538	603.037	40	Shtëpi-Ndërtesë	PM
93	7507917.434	4699799.936	602.721	40	Shtëpi-Ndërtesë	PM

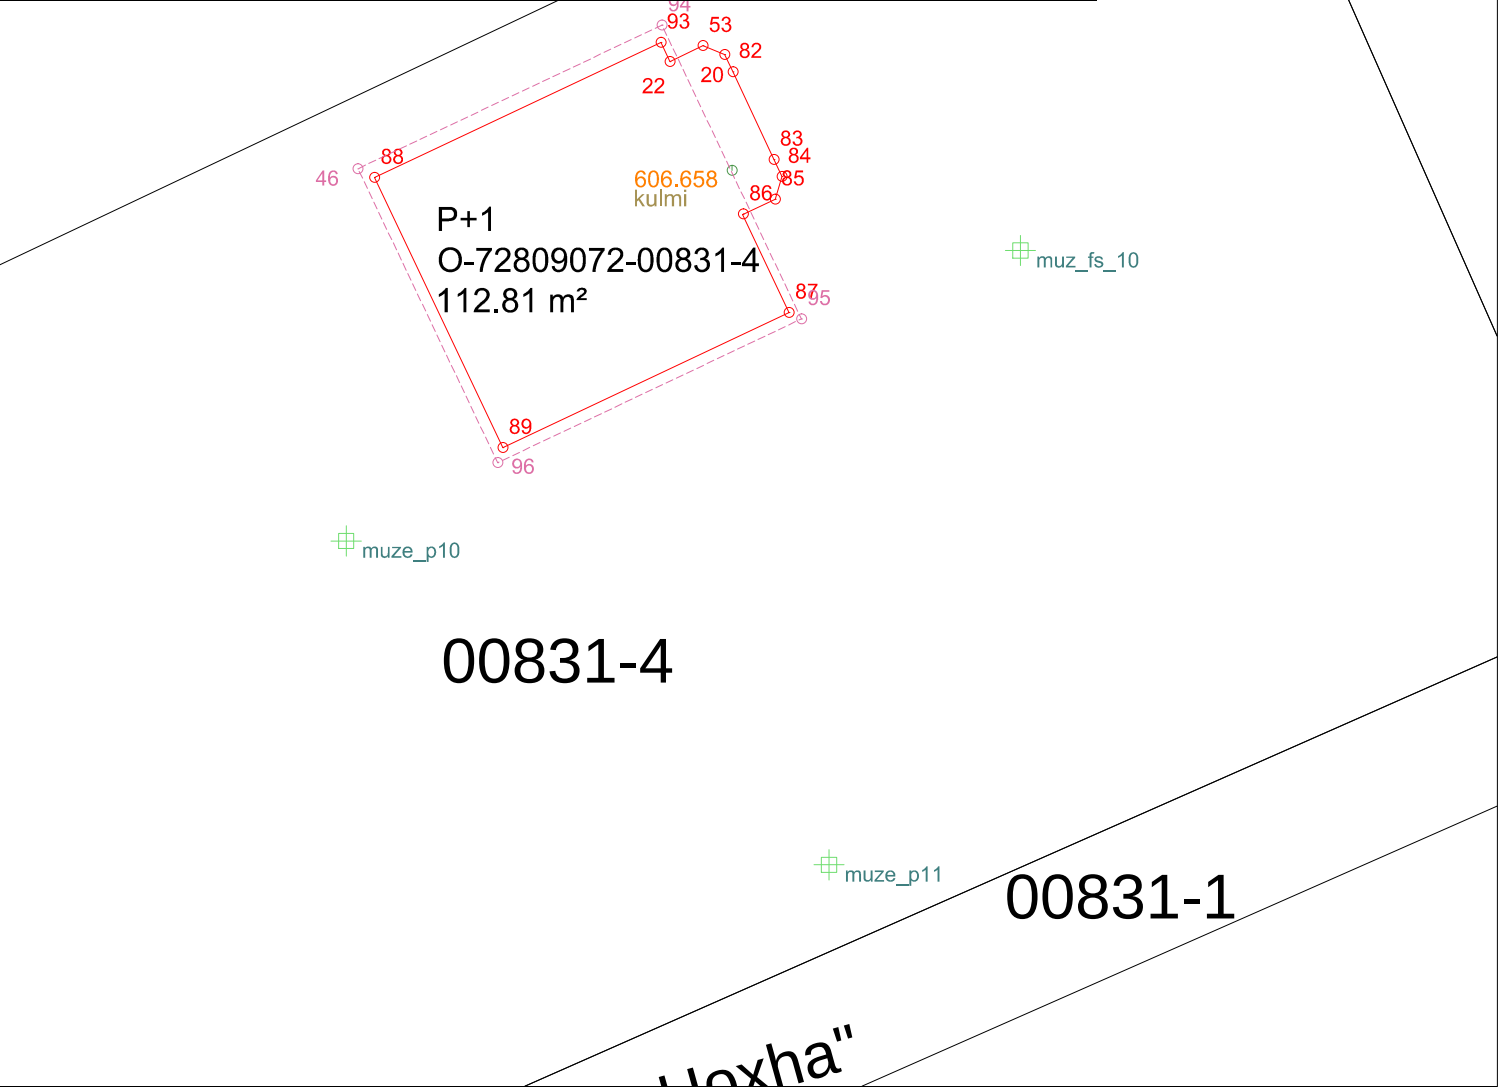



Republika e Kosovës

Qeveria - Vlada

Ministria e Mjedisit dhe Planifikimit Hapësinor / Ministarstv Sredine i Prstrng Planiranja

AGJENCIA KADASTRALE E KOSOVËS/ KATASTARSKA AGENCIJA KOSOVA



Situacioni i terrenit

Zyra kadastrale kmunale / pštinska katastarska kancelarija: Shtime

Zona kadastrale / Katastarska zona: Rashincë

Nr. i njësisë kadastrale / Br. katastarske jedinice : 00831-4

Numri i lëndës / Broj predmeta:

Shkalla e zvoglimit / Razmera plana 1: 250

Lista e koordinatave të pikave të matura:

Nr	Y	X	H	DSC
97	7507919.782	4699795.703	606.658	kulmi
3	7507897.718	4699758.912	598.122	kygjeuji
102	7507929.320	4699793.057	599.949	muz_fs_10
103	7507907.031	4699783.454	598.248	muze_p10
104	7507922.993	4699772.748	598.084	muze_p11
105	7507923.804	4699803.274	598.237	muze_p12
20	7507919.544	4699799.530	598.429	perdhese
22	7507917.736	4699799.301	598.429	perdhese
53	7507918.823	4699799.828	598.429	perdhese
82	7507919.815	4699798.965	598.316	perdhese
83	7507921.174	4699796.065	598.429	perdhese
84	7507921.437	4699795.498	598.276	perdhese
85	7507921.216	4699794.751	598.268	perdhese
86	7507920.159	4699794.259	598.286	perdhese
87	7507921.675	4699791.008	598.278	perdhese
88	7507907.971	4699795.466	598.429	perdhese
89	7507912.212	4699786.538	603.037	perdhese
93	7507917.434	4699799.936	602.721	perdhese
2	7507905.420	4699760.042	598.120	pusetFeekkal
8	7507957.699	4699783.112	598.031	pusetFeekkal
7	7507963.634	4699783.136	597.937	shtyllElektrike
46	7507907.421	4699795.761	602.788	streha
94	7507917.471	4699800.508	602.628	streha
95	7507922.080	4699790.795	602.757	streha
96	7507912.038	4699786.041	602.788	streha

Shpjegues:

Kufiri kadastral (nga SIKTK-G)

Ndërtesa në trajtim për legalizim

Ndërtesa tjera

Aneks Ndërtimi

Shtyllë elektrike

Pusetë e ujësjellësit

Pusetë e ujërave të zeza

Strehët

Kyqje në rrymë

Rilevoi / Snimi:

LIRIDON SEJDIU

(emri dhe mbiemri i gjedetit/kompanisë/ ime i prezime gedeta/ kompanije)

Nr. i licencës / Br. licence:

140

Data e rlevimit / Datum snimanja:

21.08.2025

Nënshkrimi / Potpis:

V.V.

Pikë e objekteve fqinje

Emri i rrugës

Pikë e rrjetës gjeodezike

Pikë e strehëve

Pikë e terasës

Pikë e objektit

Pikë e murit

Pikë e kulmit



Ministria e Mjedisit dhe Planifikimit Hapësinor /Ministarstvo Sredine i Prostornog Planiranja
AGJENCIA KADASTRALE E KOSOVËS/ KATASTRARSKA AGENCIJA KOSOVA

Orto 2004

Zyra kadastrale kmunale / pštinska katastarska kancelarija: Shtime

Zona kadastrale / Katastarska zona: Rashincë

Nr. i njësisë kadastrale / Br. katastarske jedinice : 00831-4

Numri i lëndës / Broj predmeta: _____

Shkalla e zvoglimit / Razmera plana 1: 250

Lista e koordinatave të pikave të matura:

Nr	Y	X	H	DSC
97	7507919.782	4699795.703	606.658	kulmi
3	7507897.718	4699758.912	598.122	kyqjeuji
102	7507929.320	4699793.057	599.949	muz fs 10
103	7507907.031	4699783.454	598.248	mize p10
104	7507922.993	4699772.748	598.084	muze p11
105	7507923.804	4699803.274	598.237	mize p12
20	7507919.544	4699799.530	598.429	perdhese
22	7507917.736	4699799.301	598.429	perdhese
53	7507918.823	4699799.828	598.429	perdhese
82	7507919.815	4699798.965	598.316	perdhese
83	7507921.174	4699796.065	598.429	perdhese
84	7507921.437	4699795.498	598.276	perdhese
85	7507921.216	4699794.751	598.268	perdhese
86	7507920.159	4699794.259	598.286	perdhese
87	7507921.675	4699791.008	598.278	perdhese
88	7507907.971	4699795.466	598.429	perdhese
89	7507912.212	4699786.538	603.037	perdhese
93	7507917.434	4699799.936	602.721	perdhese
2	7507905.420	4699760.042	598.120	pusetFeekkal
8	7507957.699	4699783.112	598.031	pusetFeekkal
7	7507963.634	4699783.136	597.937	shyElektri
46	7507907.421	4699795.761	602.788	streha
94	7507917.471	4699800.508	602.628	streha
95	7507922.080	4699790.795	602.757	streha
96	7507912.038	4699786.041	602.788	streha

Shpjegues:

-  Kufiri kadastral (nga SIKTK-G)
-  Ndërtesa në trajtim për legalizim
-  Ndërtesa tjera
-  Aneks Ndërtimi
-  Shtyllë elektrike
-  Pusëtë e ujësjellësit
-  Pusëtë e ujërave të zeza
-  Strehët
-  Kyqje në rrymë

Pikë e objekteve fqinje	
Rr. Emri i rrugës	
Pikë e rrjetës gjeodezike	
Pikë e strehëve	
Pikë e terasës	
Pikë e objektit	
Pikë e murit	
Pikë e kulmit	

Rilevoi / Snimi: LIRIDON SEJDIU

(emri dhe mbiemri i gjedetit/kompanisë/ ime i prezime gedeta/ kompanije)

Nr. i licencēs / Br. licence: 140

Data e rilevimit / Datum snimanja: 21.08.2025

Nënshkrimi / Potpis: _____

V.V.

331-1

10



Oeveria -Vlada

AGJENCIA KADASTRALE E KOSOVËS/ KATASTARSKA AGENCIJA KOSOVA

Orto 2018

Zona kadastrale / Katastarska zona: Rashincë

Nr. i njësisë kadastrale / Br. katastarske jedinice : 00831-4

Numri i lëndës / Broj predmeta:

Shkalla e zvoglimit / Razmera plana 1: 250

Nr	Y	X	H	DSC ^c
97	7507919.782	4699795.703	606.658	kulmi
3	7507897.718	4699758.912	598.122	kyqjeuji
102	7507929.320	4699793.057	599.949	muz fs_10
103	7507907.031	4699783.454	598.248	muze_p10
104	7507922.993	4699772.748	598.084	muze_p11
105	7507923.804	4699803.274	598.237	muze_p12
20	7507919.544	4699799.530	598.429	perdhese
22	7507917.736	4699799.301	598.429	perdhese
53	7507918.823	4699799.828	598.429	perdhese
82	7507919.815	4699798.965	598.316	perdhese
83	7507921.174	4699796.065	598.429	perdhese
84	7507921.437	4699795.498	598.276	perdhese
85	7507921.216	4699794.751	598.268	perdhese
86	7507920.159	4699794.259	598.286	perdhese
87	7507921.675	4699791.008	598.278	perdhese
88	7507907.971	4699795.466	598.429	perdhese
89	7507912.212	4699786.538	603.037	perdhese
93	7507917.434	4699799.936	602.721	perdhese
2	7507905.420	4699760.042	598.120	pusetFeekkal
8	7507957.699	4699783.112	598.031	pusetFeekkal
7	7507963.634	4699783.136	597.937	shtylElektrike
46	7507907.421	4699795.761	602.788	streha
94	7507917.471	4699800.598	602.628	streha
95	7507922.080	4699790.795	602.757	streha
96	7507912.038	4699786.041	602.788	streha

- Kufiri kadastral (nga SIKTK-G)
- Ndërtesa në trajtim për legalizim
- Ndërtesa tjera
- Aneks Ndërtimi
- Shtyllë elektrike
- Pusëtë e ujës/jellësit
- Pusëtë e ujërave të zeza
- Strehët
- Kyqje në rrymë

Rilevoi / Snimi: LIRIDON SEJDIU

(emri dhe mbiemri i gjedetit/kompanisë/ ime i prezime gedeta/ kompanije)

Nr. i licencēs / Br. licence: 140

Data e rilevimit / Datum snimanja: 21.08.2025

Nënshkrimi / Potpis:

V.V.

Pikë e objekteve fqinje

Rr. Emri i rrugës

Pikë e rrjetës gjeodezike

Pikë e strehëve

Pikë e terasës

Pikë e objektit

Pikë e murit

Pikë e kulmit





Republika e Kosovës
Republika Kosova-Republic of Kosovo
Qeveria e Kosovës- Vlada Kosova- Government of Kosovo
Ministria e Infrastrukturës dhe Ambientit/ Ministrastvo Infrastrukture i Sredine/ Ministry of Infrastructure and Environment
AGJENCIA KADASTRALE E KOSOVËS/KOSOVSKA KATASTARSKA AGENCIJA/ KOSOVO CADASTRAL AGENCY

Komuna: Shtime	Zona Kadastrale: Rashincë
Numri i njësis kadastrale: 00831-4	Sistemi koordinat: KosovaRef01

Nr	Y	X	H	Kodi	Përshkrimi	Burimi
20	7507919.544	4699799.530	598.429	40	Shtëpi-Ndërtesë	PM
22	7507917.736	4699799.301	598.429	40	Shtëpi-Ndërtesë	PM
53	7507918.823	4699799.828	598.429	40	Shtëpi-Ndërtesë	PM
82	7507919.815	4699798.965	598.316	40	Shtëpi-Ndërtesë	PM
83	7507921.174	4699796.065	598.429	40	Shtëpi-Ndërtesë	PM
84	7507921.437	4699795.498	598.276	40	Shtëpi-Ndërtesë	PM
85	7507921.216	4699794.751	598.268	40	Shtëpi-Ndërtesë	PM
86	7507920.159	4699794.259	598.286	40	Shtëpi-Ndërtesë	PM
87	7507921.675	4699791.008	598.278	40	Shtëpi-Ndërtesë	PM
88	7507907.971	4699795.466	598.429	40	Shtëpi-Ndërtesë	PM
89	7507912.212	4699786.538	603.037	40	Shtëpi-Ndërtesë	PM
93	7507917.434	4699799.936	602.721	40	Shtëpi-Ndërtesë	PM

Gjeodeti / Kompania gjeodete e licencuar:	Liridon Sejdiu	Nënshkrimi dhe vula:	
Numri i licencës	140		

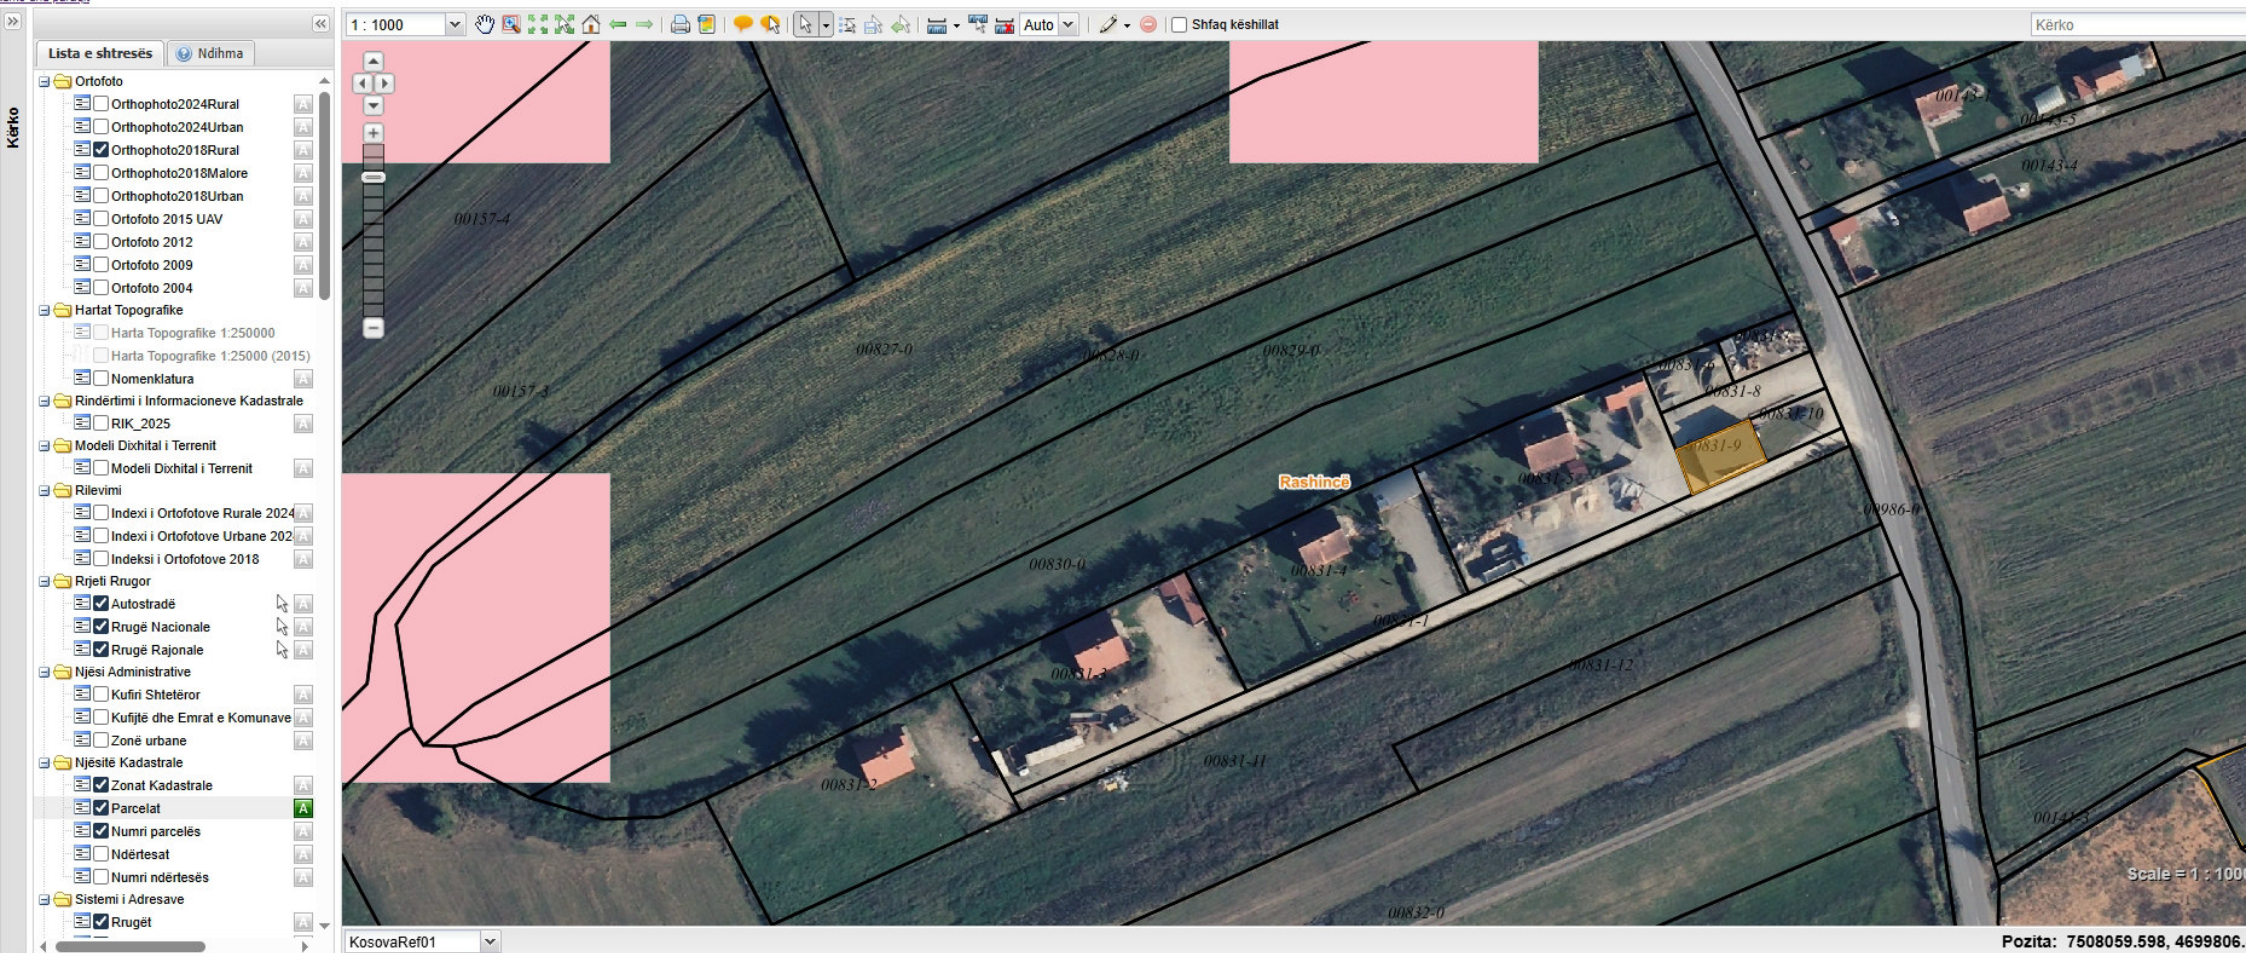

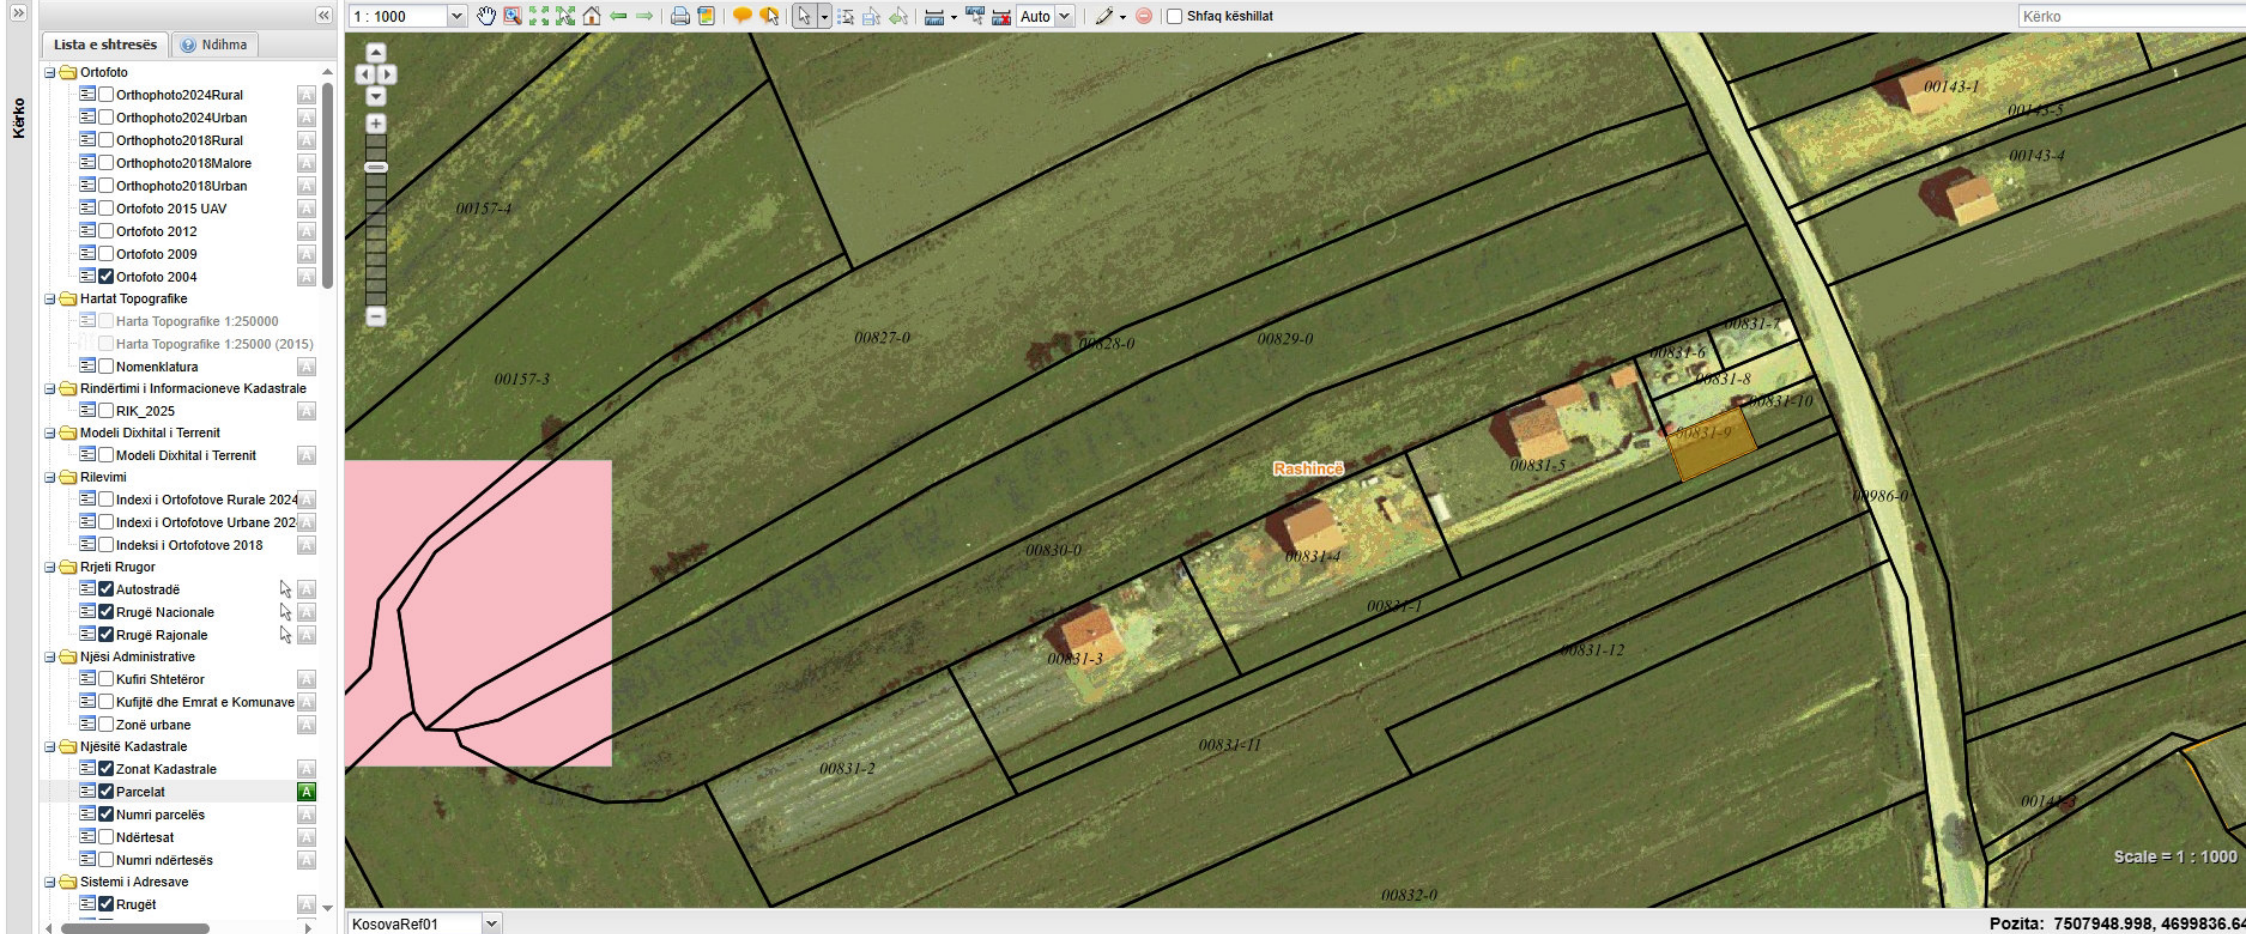

Republika e Kosovës


Republika Kosova-Republic of Kosova

Qeveria -Vlada-Government

Ministria e Mjedisit dhe Planifikimit Hapësinor /Ministarstvo Sredine i Prostornog Planiranja/Ministry of Environment and Spatial Planning

AGJENCIA KADASTRALE E KOSOVËS/ KATASTARSKA AGENCIJA KOSOVA/ KOSOVA CADASTRAL AGENCY

Nr.	Y	X	H	D	Etazhi	Sqarim	Sipërfaqja (m²)
20	7507919.54	4699799.53	598.43	perdhese	Përdhesa	Përdhesa	112.81
22	7507917.74	4699799.30	598.43	perdhese			
53	7507918.82	4699799.83	598.43	perdhese			
82	7507919.82	4699798.97	598.32	perdhese			
83	7507921.17	4699796.07	598.43	perdhese			
84	7507921.44	4699795.50	598.28	perdhese			
85	7507921.22	4699794.75	598.27	perdhese			
86	7507920.16	4699794.26	598.29	perdhese			
87	7507921.68	4699791.01	598.28	perdhese			
88	7507907.97	4699795.47	598.43	perdhese			
89	7507912.21	4699786.54	603.04	perdhese			
93	7507917.43	4699799.94	602.72	perdhese			
						Gjithsej:	112.81

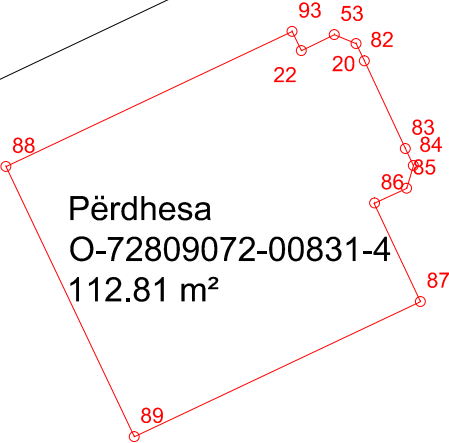

00831-4

00831-1
Rr. "Maliq Hoxha"


Republika e Kosovës

Republika Kosova-Republic of Kosova

Qeveria -Vlada-Government

Ministria e Mjedisit dhe Planifikimit Hapësinor /Ministarstvo Sredine i Prostornog Planiranja/Ministry of Environment and Spatial Planning

AGJENCIA KADASTRALE E KOSOVËS/ KATASTARSKA AGENCIJA KOSOVA/ KOSOVA CADASTRAL AGENCY

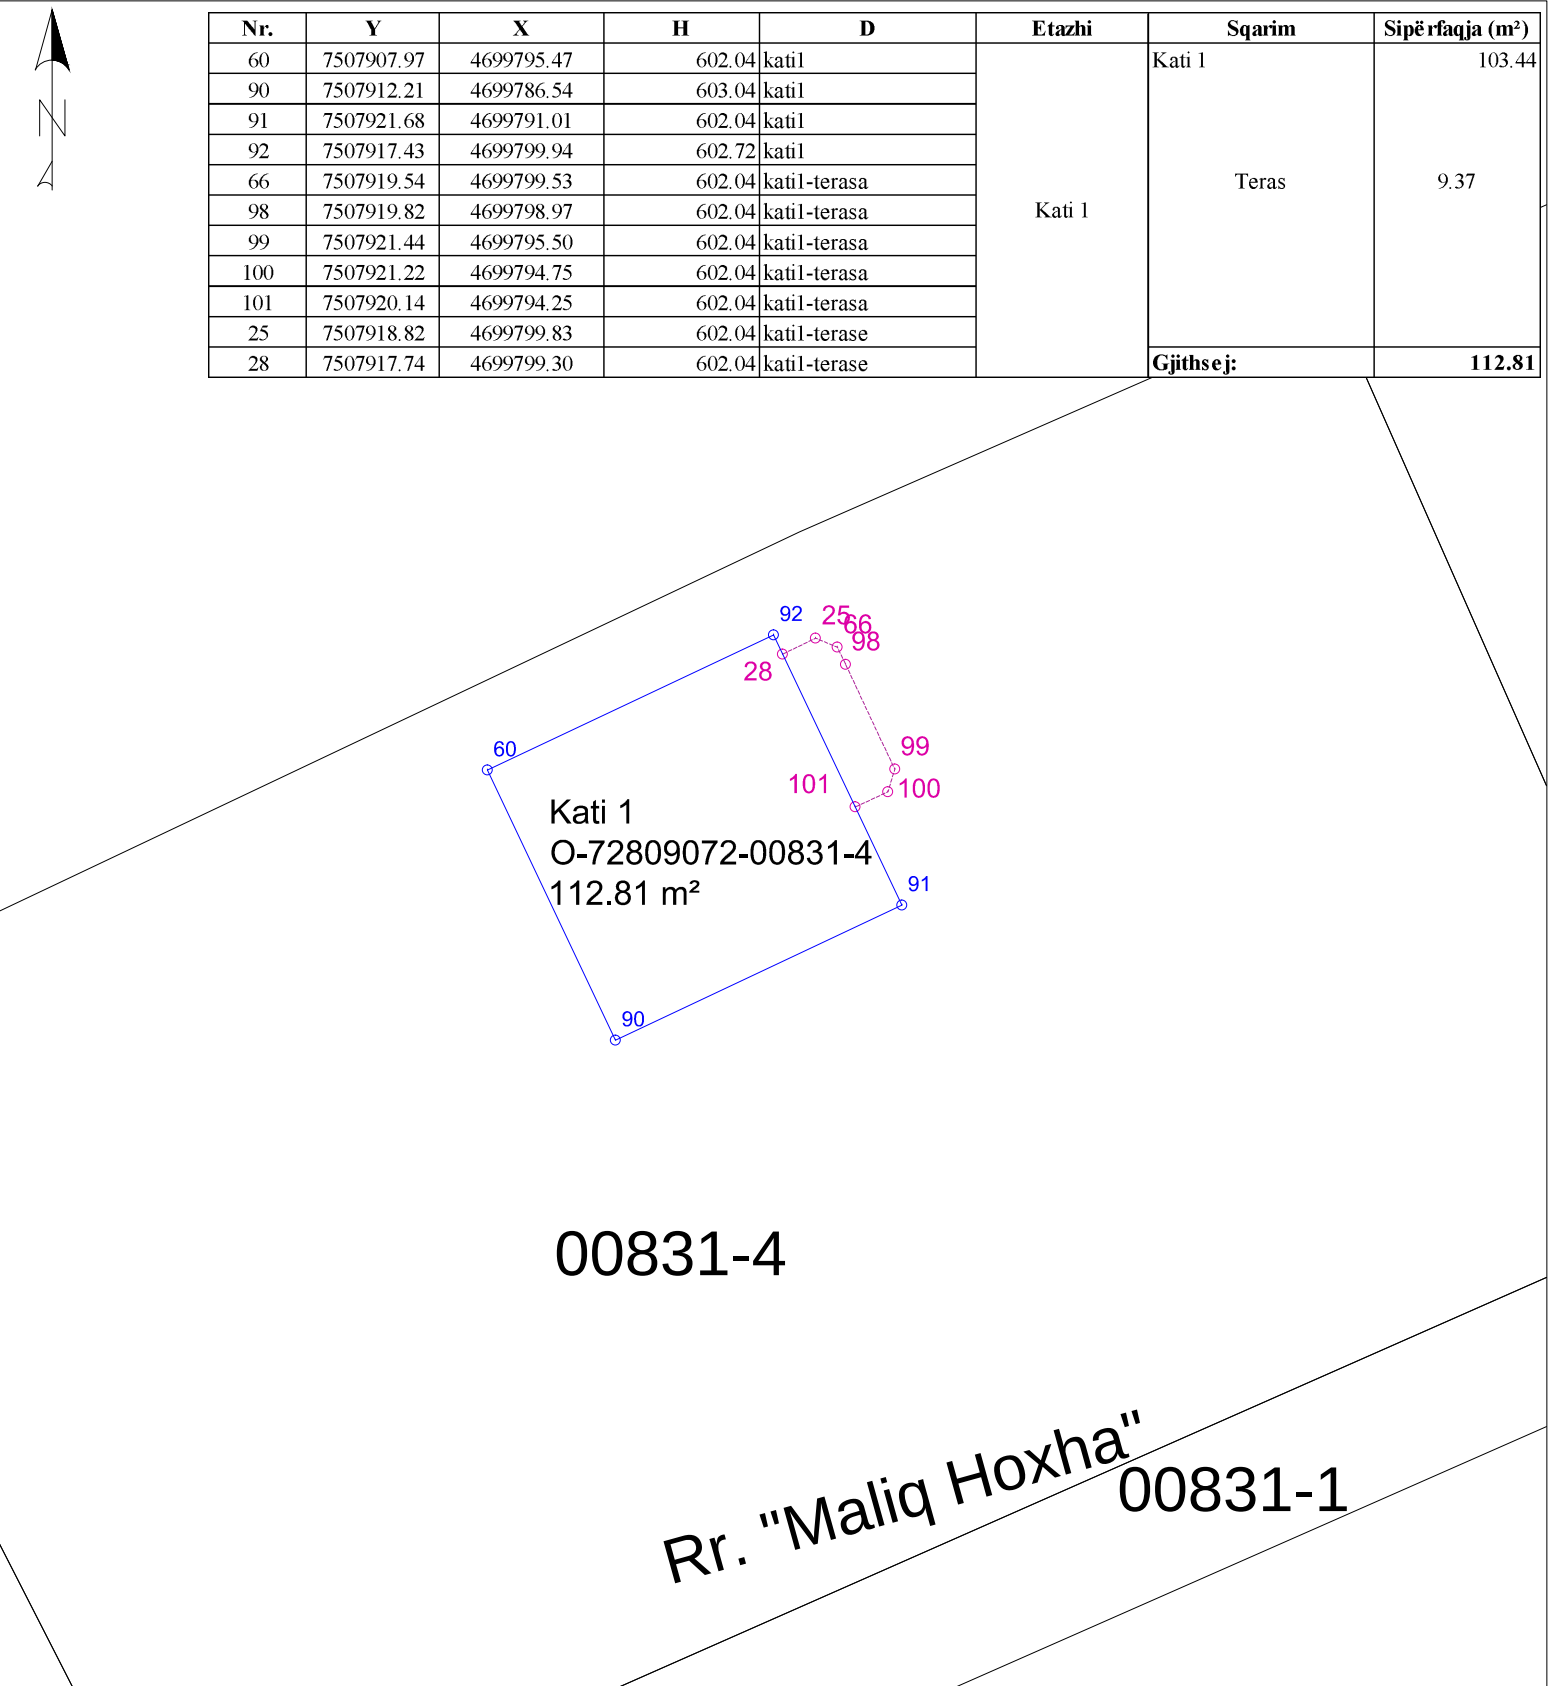

00831-4

Rr. "Maliq Hoxha"

00831-1



Republika e Kosovës
Republika Kosova-Republic of Kosovo
Qeveria e Kosovës- Vlada Kosova- Government of Kosovo
Ministria e Infrastrukturës dhe Ambientit/ Ministrastvo Infrastrukture i Sredine/ Ministry of Infrastructure and Environment
AGJENCIA KADASTRALE E KOSOVËS/KOSOVSKA KATASTARSKA AGENCIJA/ KOSOVO CADASTRAL AGENCY

Komuna: Shtime
Numri i njësis kadastrale: 00831-4

Zona Kadastrale: Rashincë
Sistemi koordinat: KosovaRef01

Nr.	Y	X	H	D	Etazhi	Sqarim	Sipërfaqja (m ²)
20	7507919.54	4699799.53	598.43	perdhese	Përdhesa	Përdhesa	112.81
22	7507917.74	4699799.30	598.43	perdhese			
53	7507918.82	4699799.83	598.43	perdhese			
82	7507919.82	4699798.97	598.32	perdhese			
83	7507921.17	4699796.07	598.43	perdhese			
84	7507921.44	4699795.50	598.28	perdhese			
85	7507921.22	4699794.75	598.27	perdhese			
86	7507920.16	4699794.26	598.29	perdhese			
87	7507921.68	4699791.01	598.28	perdhese			
88	7507907.97	4699795.47	598.43	perdhese			
89	7507912.21	4699786.54	603.04	perdhese			
93	7507917.43	4699799.94	602.72	perdhese		Gjithsej:	112.81

Nr.	Y	X	H	D	Etazhi	Sqarim	Sipërfaqja (m ²)
60	7507907.97	4699795.47	602.04	kati 1	Kati 1	Kati 1	103.44
90	7507912.21	4699786.54	603.04	kati 1		Teras	9.37
91	7507921.68	4699791.01	602.04	kati 1			
92	7507917.43	4699799.94	602.72	kati 1			
66	7507919.54	4699799.53	602.04	kati 1-terasa			
98	7507919.82	4699798.97	602.04	kati 1-terasa			
99	7507921.44	4699795.50	602.04	kati 1-terasa			
100	7507921.22	4699794.75	602.04	kati 1-terasa			
101	7507920.14	4699794.25	602.04	kati 1-terasa			
25	7507918.82	4699799.83	602.04	kati 1-terase			
28	7507917.74	4699799.30	602.04	kati 1-terase		Gjithsej:	112.81


Gjeodeti / Kompania gjeodete e licencuar:	Liridon Sejdiu	Nënshkrimi dhe vula:	
Numri i licencës	140		



Republika e Kosovës
Republika Kosova-Republic of Kosova
Qeveria -Vlada-Government

Ministria e Mjedisit dhe Planifikimit Hapësinor /Ministarstvo Sredine i Prostornog Planiranja/Ministry of Environment and Spatial Planning
AGJENCIA KADASTRALE E KOSOVËS/ KATASTARSKA AGENCIJA KOSOVA/ KOSOVA CADASTRAL AGENCY

Nr	Y	X	H	Kodi	Përshkrimi	Burimi
20	7507919.544	4699799.530	598.429	40	Shtëpi-Ndërtesë	PM
22	7507917.736	4699799.301	598.429	40	Shtëpi-Ndërtesë	PM
53	7507918.823	4699799.828	598.429	40	Shtëpi-Ndërtesë	PM
82	7507919.815	4699798.965	598.316	40	Shtëpi-Ndërtesë	PM
83	7507921.174	4699796.065	598.429	40	Shtëpi-Ndërtesë	PM
84	7507921.437	4699795.498	598.276	40	Shtëpi-Ndërtesë	PM
85	7507921.216	4699794.751	598.268	40	Shtëpi-Ndërtesë	PM
86	7507920.159	4699794.259	598.286	40	Shtëpi-Ndërtesë	PM
87	7507921.675	4699791.008	598.278	40	Shtëpi-Ndërtesë	PM
88	7507907.971	4699795.466	598.429	40	Shtëpi-Ndërtesë	PM
89	7507912.212	4699786.538	603.037	40	Shtëpi-Ndërtesë	PM
93	7507917.434	4699799.936	602.721	40	Shtëpi-Ndërtesë	PM

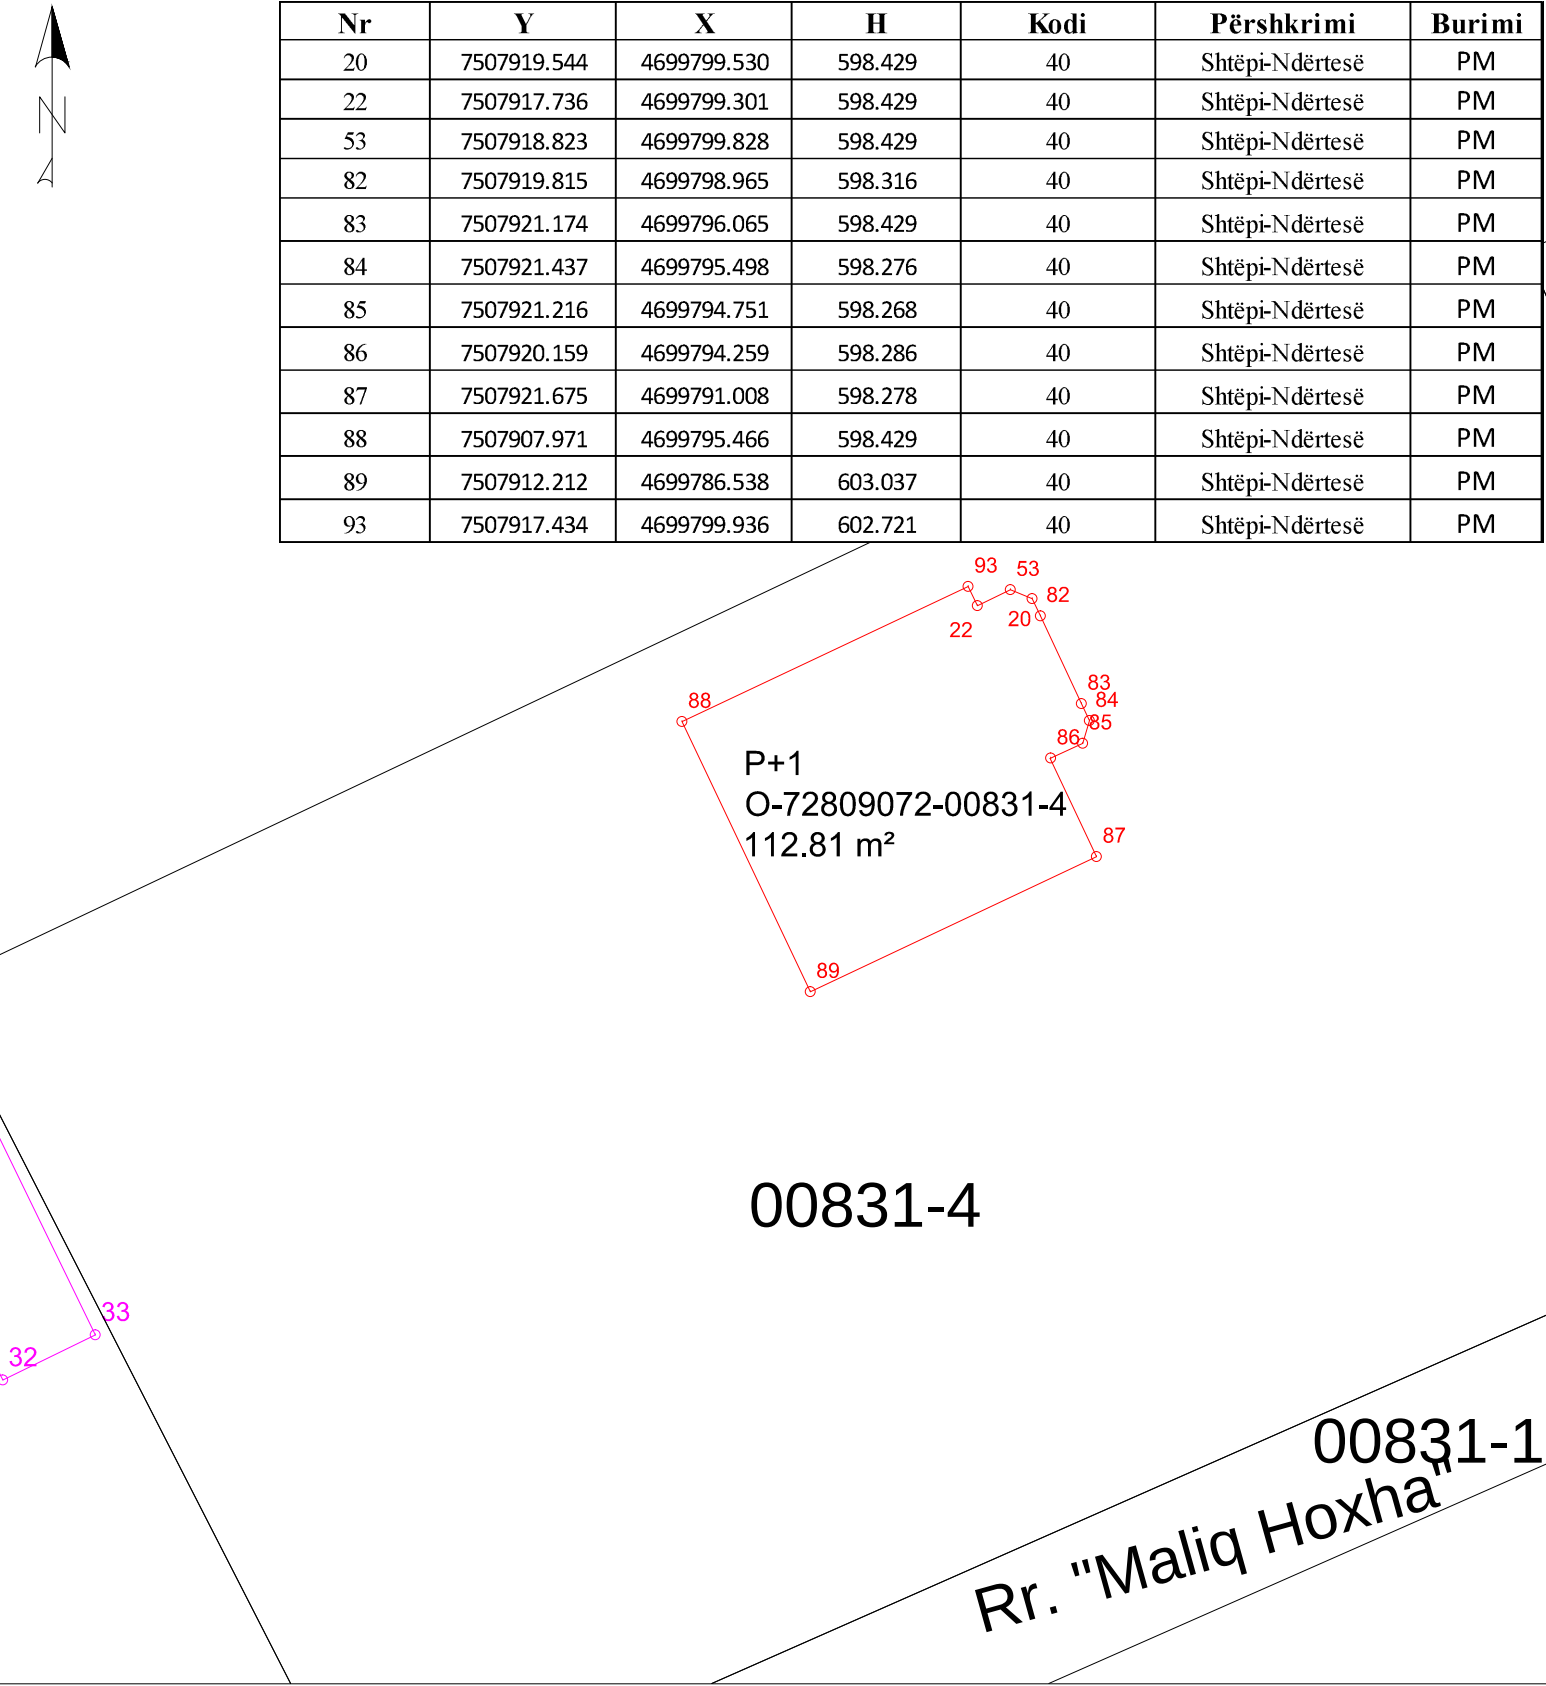



Republika e Kosovës

Republika Kosova-Republic of Kosovo

Qeveria e Kosovës- Vlada Kosova- Government of Kosovo

Ministria e Infrastrukturës dhe Ambientit/ Ministrastvo Infrastrukture i Sredine/ Ministry of Infrastructure and Environment

AGJENCIA KADASTRALE E KOSOVËS/KOSOVSKA KATASTARSKA AGENCIJA/ KOSOVO CADASTRAL AGENCY

Komuna: Shtime

Numri i njësis kadastrale: 00831-4

Zona Kadastrale: Rashincë

Sistemi koordinat: KosovaRef01

Nr	Y	X	H	Kodi	Përshkrimi	Burimi
20	7507919.544	4699799.530	598.429	40	Shtëpi-Ndërtesë	PM
22	7507917.736	4699799.301	598.429	40	Shtëpi-Ndërtesë	PM
53	7507918.823	4699799.828	598.429	40	Shtëpi-Ndërtesë	PM
82	7507919.815	4699798.965	598.316	40	Shtëpi-Ndërtesë	PM
83	7507921.174	4699796.065	598.429	40	Shtëpi-Ndërtesë	PM
84	7507921.437	4699795.498	598.276	40	Shtëpi-Ndërtesë	PM
85	7507921.216	4699794.751	598.268	40	Shtëpi-Ndërtesë	PM
86	7507920.159	4699794.259	598.286	40	Shtëpi-Ndërtesë	PM
87	7507921.675	4699791.008	598.278	40	Shtëpi-Ndërtesë	PM
88	7507907.971	4699795.466	598.429	40	Shtëpi-Ndërtesë	PM
89	7507912.212	4699786.538	603.037	40	Shtëpi-Ndërtesë	PM
93	7507917.434	4699799.936	602.721	40	Shtëpi-Ndërtesë	PM

Gjeodeti / Kompania gjeodete e licencuar:	Liridon Sejdiu	Nënshkrimi dhe vula:	
Numri i licencës	140		



Republika e Kosovës
Republika Kosova - Republic of Kosovo
Qeveria e Kosovës - Vlada Kosova - Government of Kosovo
Ministria e Infrastrukturës dhe Ambientit/ Ministrastvo Infrastrukture i Sredine/ Ministry of Infrastructure and Environment
AGJENCIA KADASTRALE E KOSOVËS/ KOSOVSKA KATASTARSKA AGENCIJA/ KOSOVA CADASTRAL AGENCY

R E G J I S T R I M I I N D E R T E S Ë S / S H T Ë P I S Ë													
Nr	Komuna	Zona Kadastrale	Numri i ndërtesës (njësia)	Etazhiteti	Katet	Sipërfaqja e kateve [m²]	Sipërfaqja e bazamentit [m²]	Adresa e Njesisë	Vendi i quajtur	Shfrytëzimi i aktual	Pronari / Shfrytëzuesi Emri (Emri i prindit) Mbiemri	Numri personal	Pjesa e Pronës
1	SHTIME	Rashincë	O-72809072-00831-4-___-0	P+1	Përdhesa	112.81	112.81	Rr. "Maliq Hoxha" Fsh. Rashincë- SHTIME	TËRBESH	Banim	Bedri (Nazif) Salihaj	1004963209	1/1
					Kati 1	112.81							
					Gjithsej:	112.81							

Gjeodeti/kompania e licencuar: LIRIDON SEJDIU	Nr i licencës: 140	Nënshkrimi dhe vula:
---	--------------------	----------------------







